

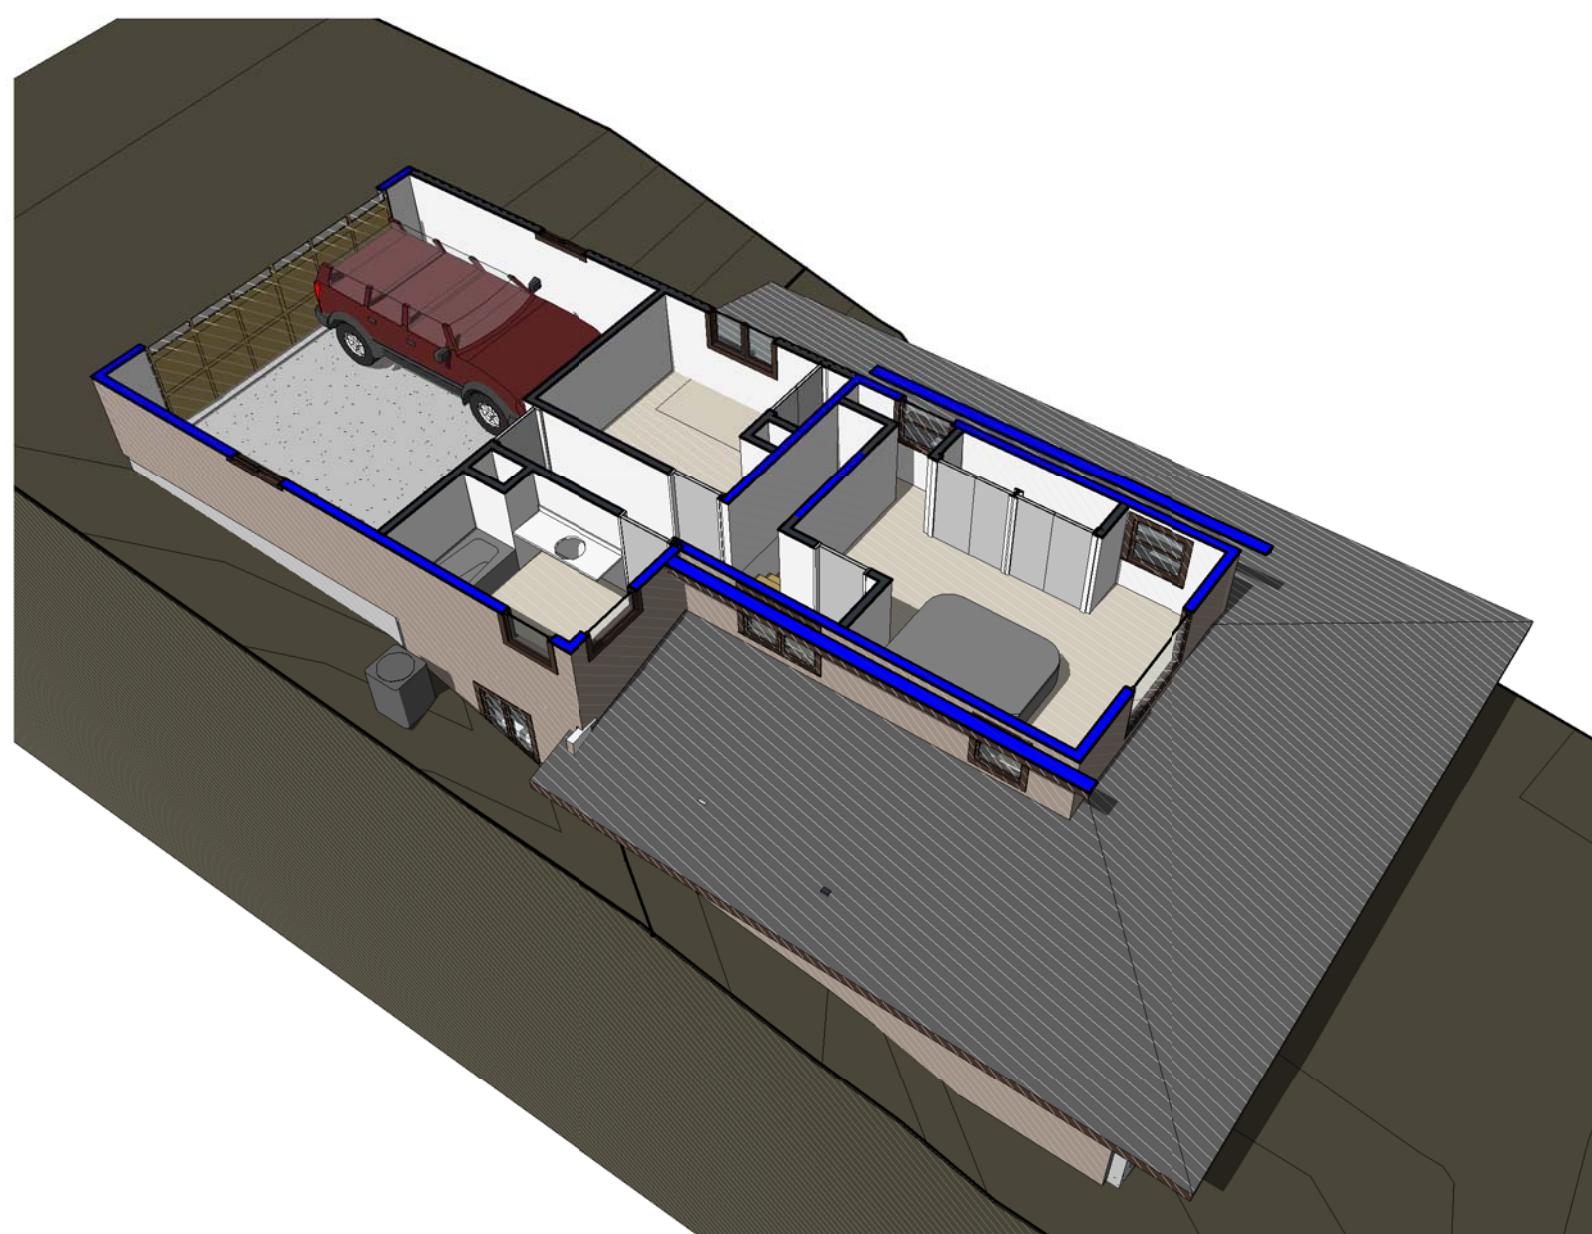


1ST & 2nd Floor  
**A102**


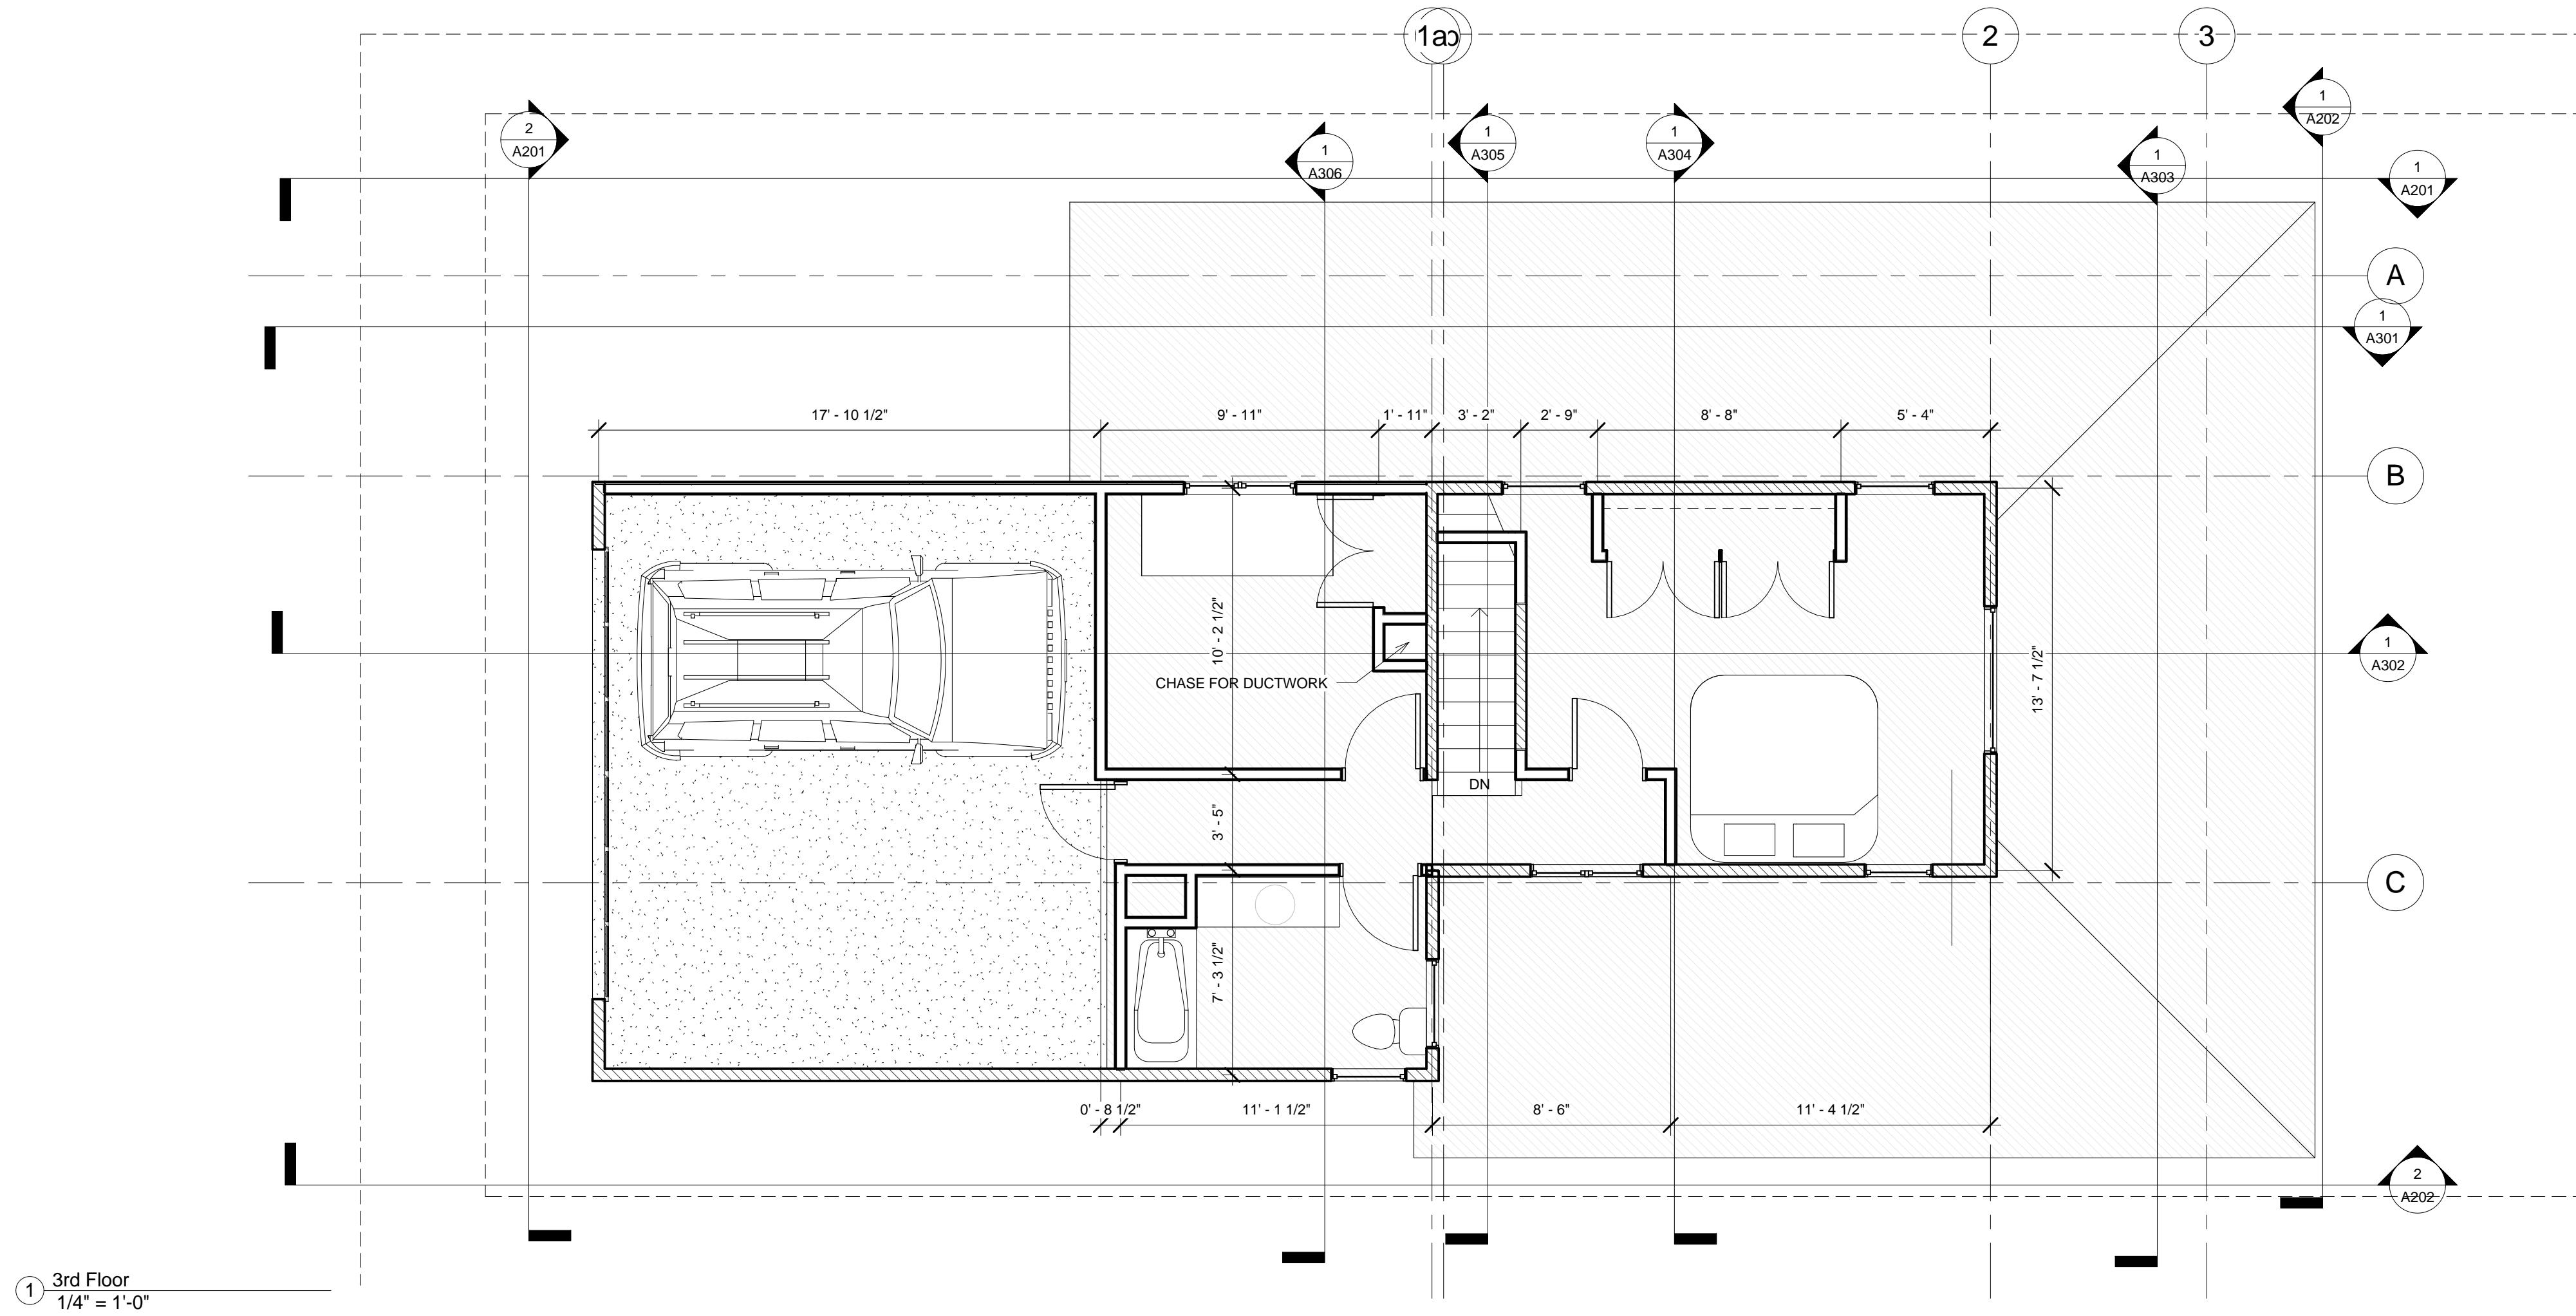


2 3rd Floor - Perspective\_1


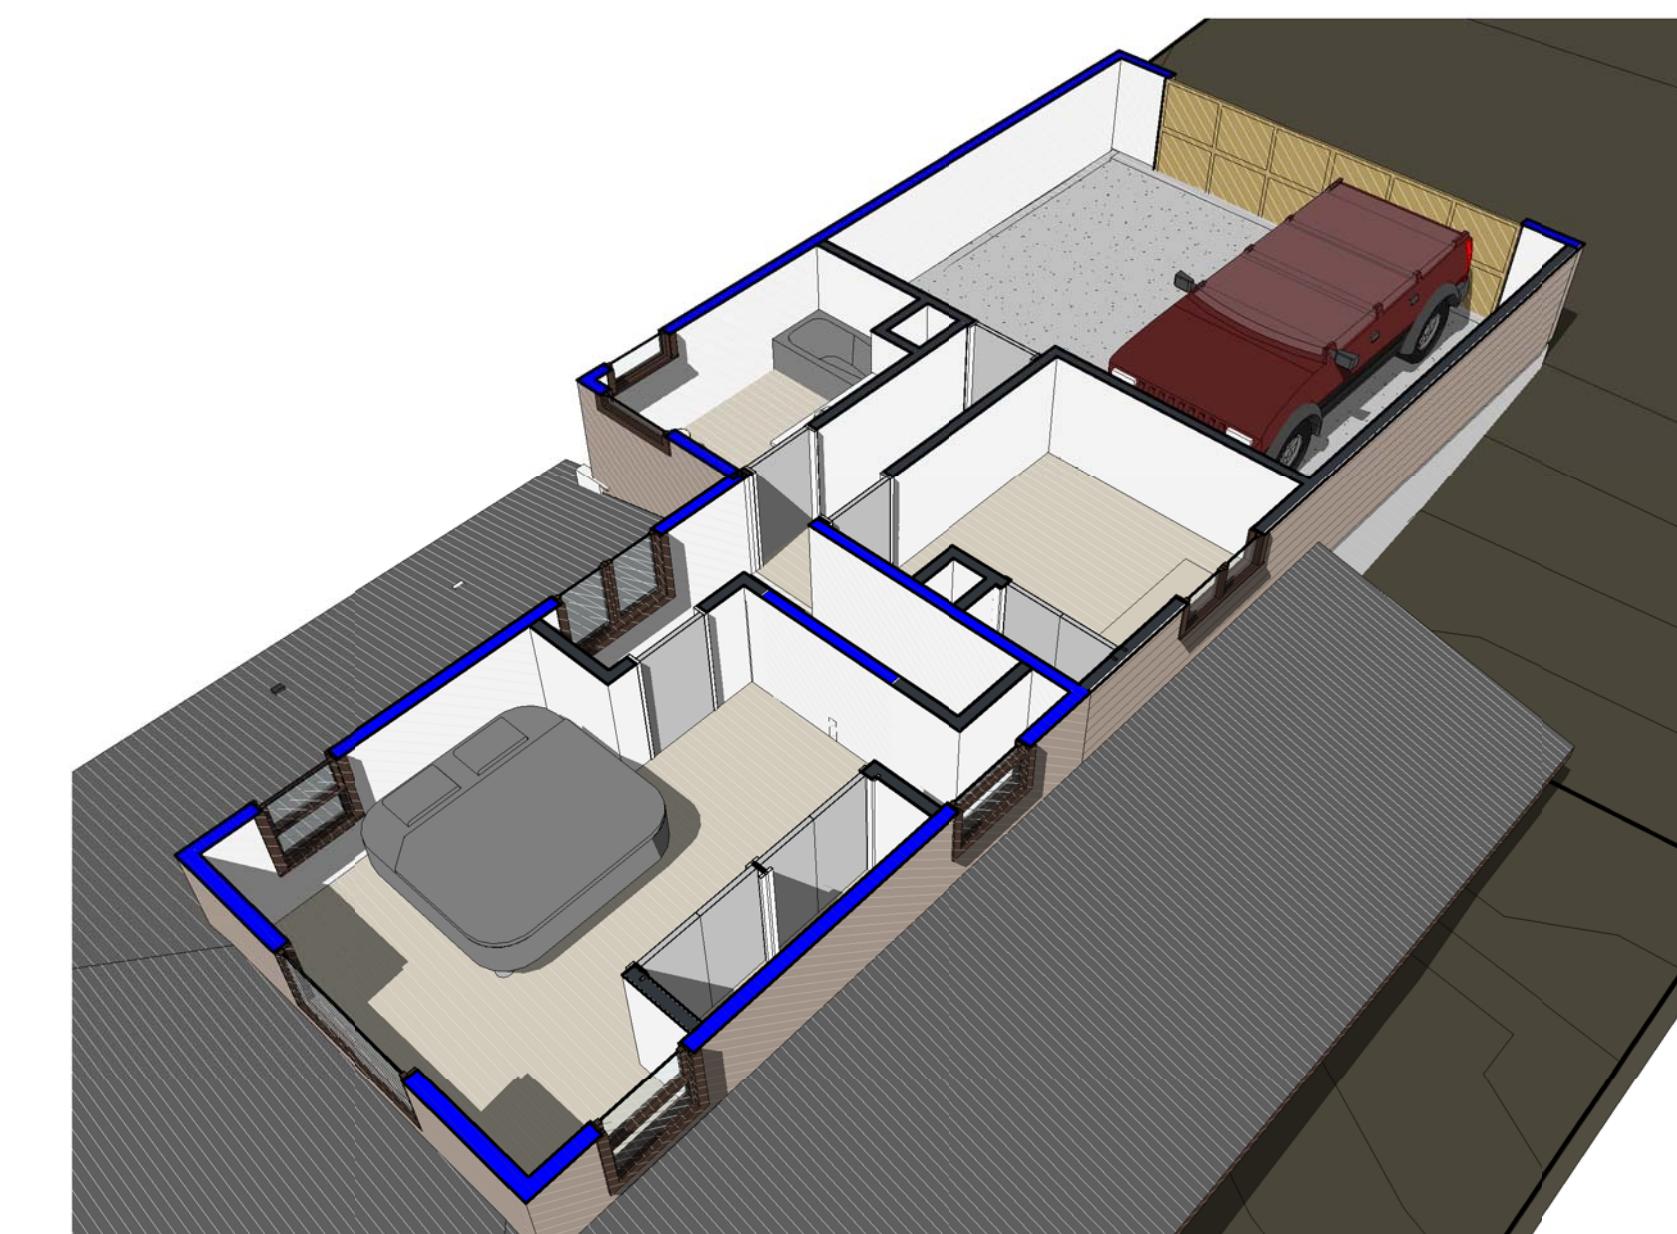


3 3rd Floor - Perspective\_2



Third Floor  
**A103**

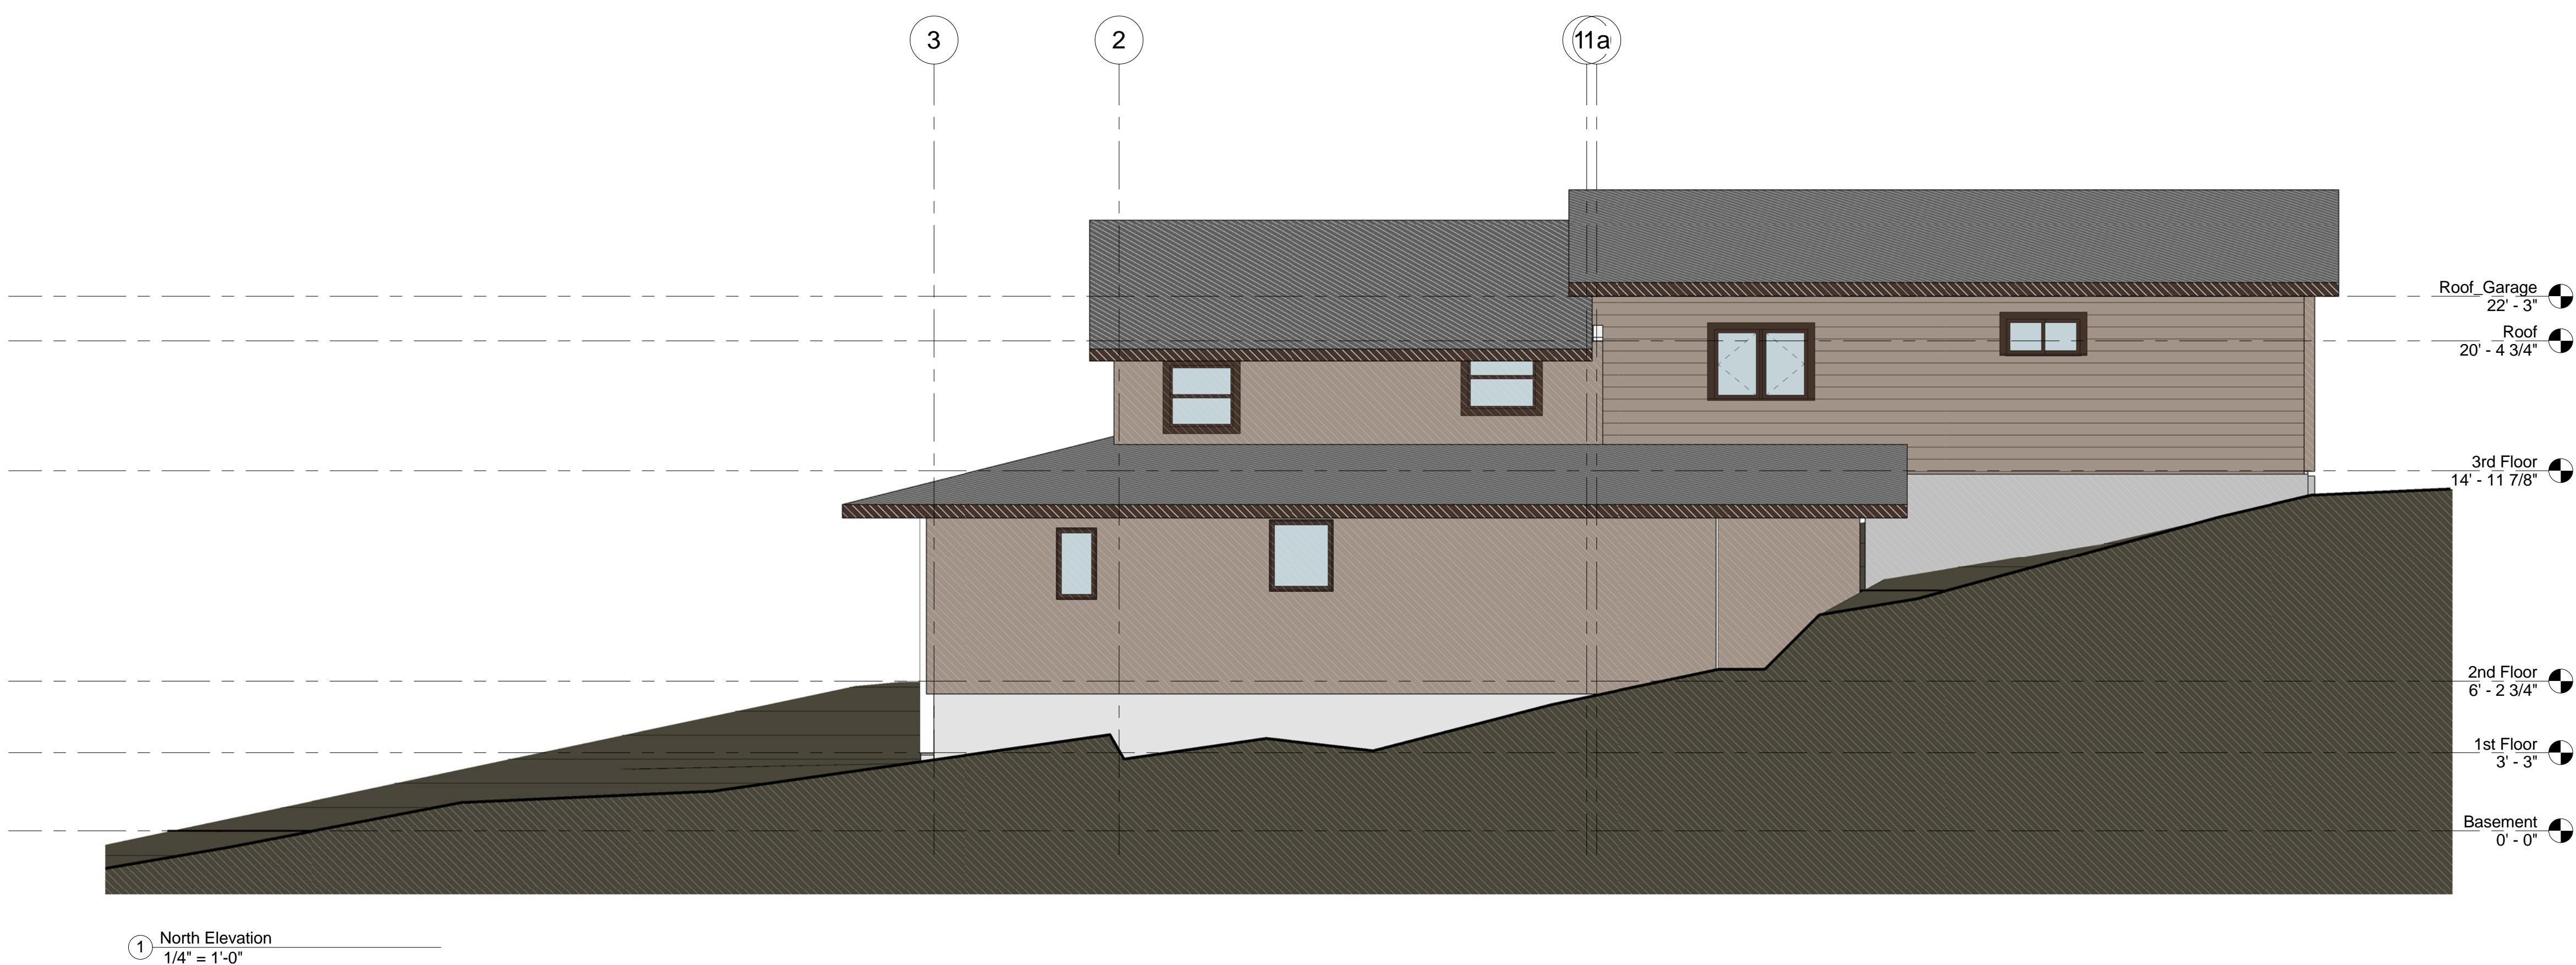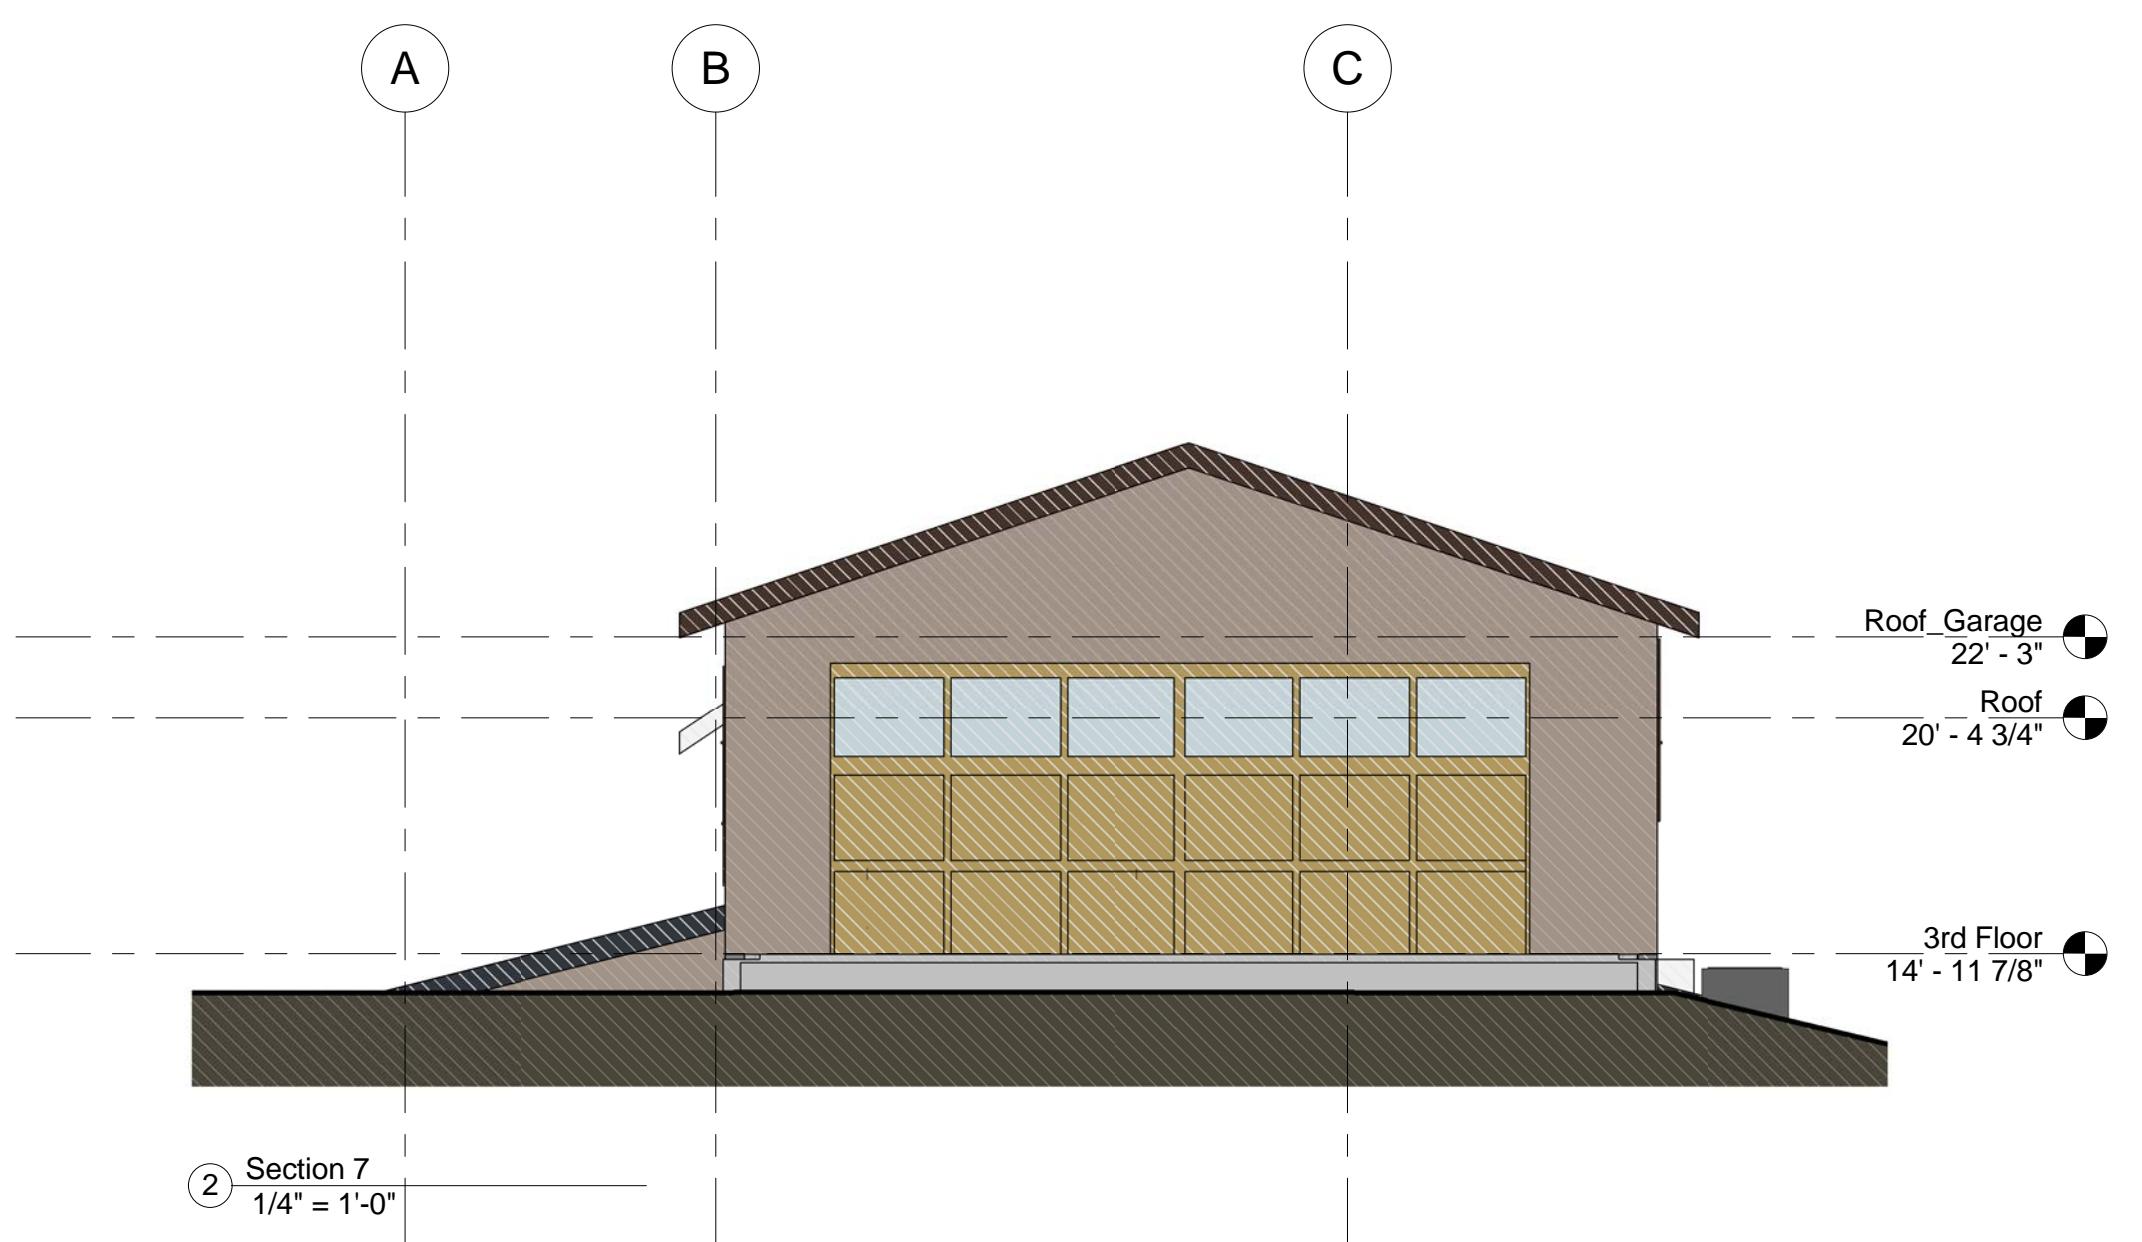



Elevations - North & West  
**A201**

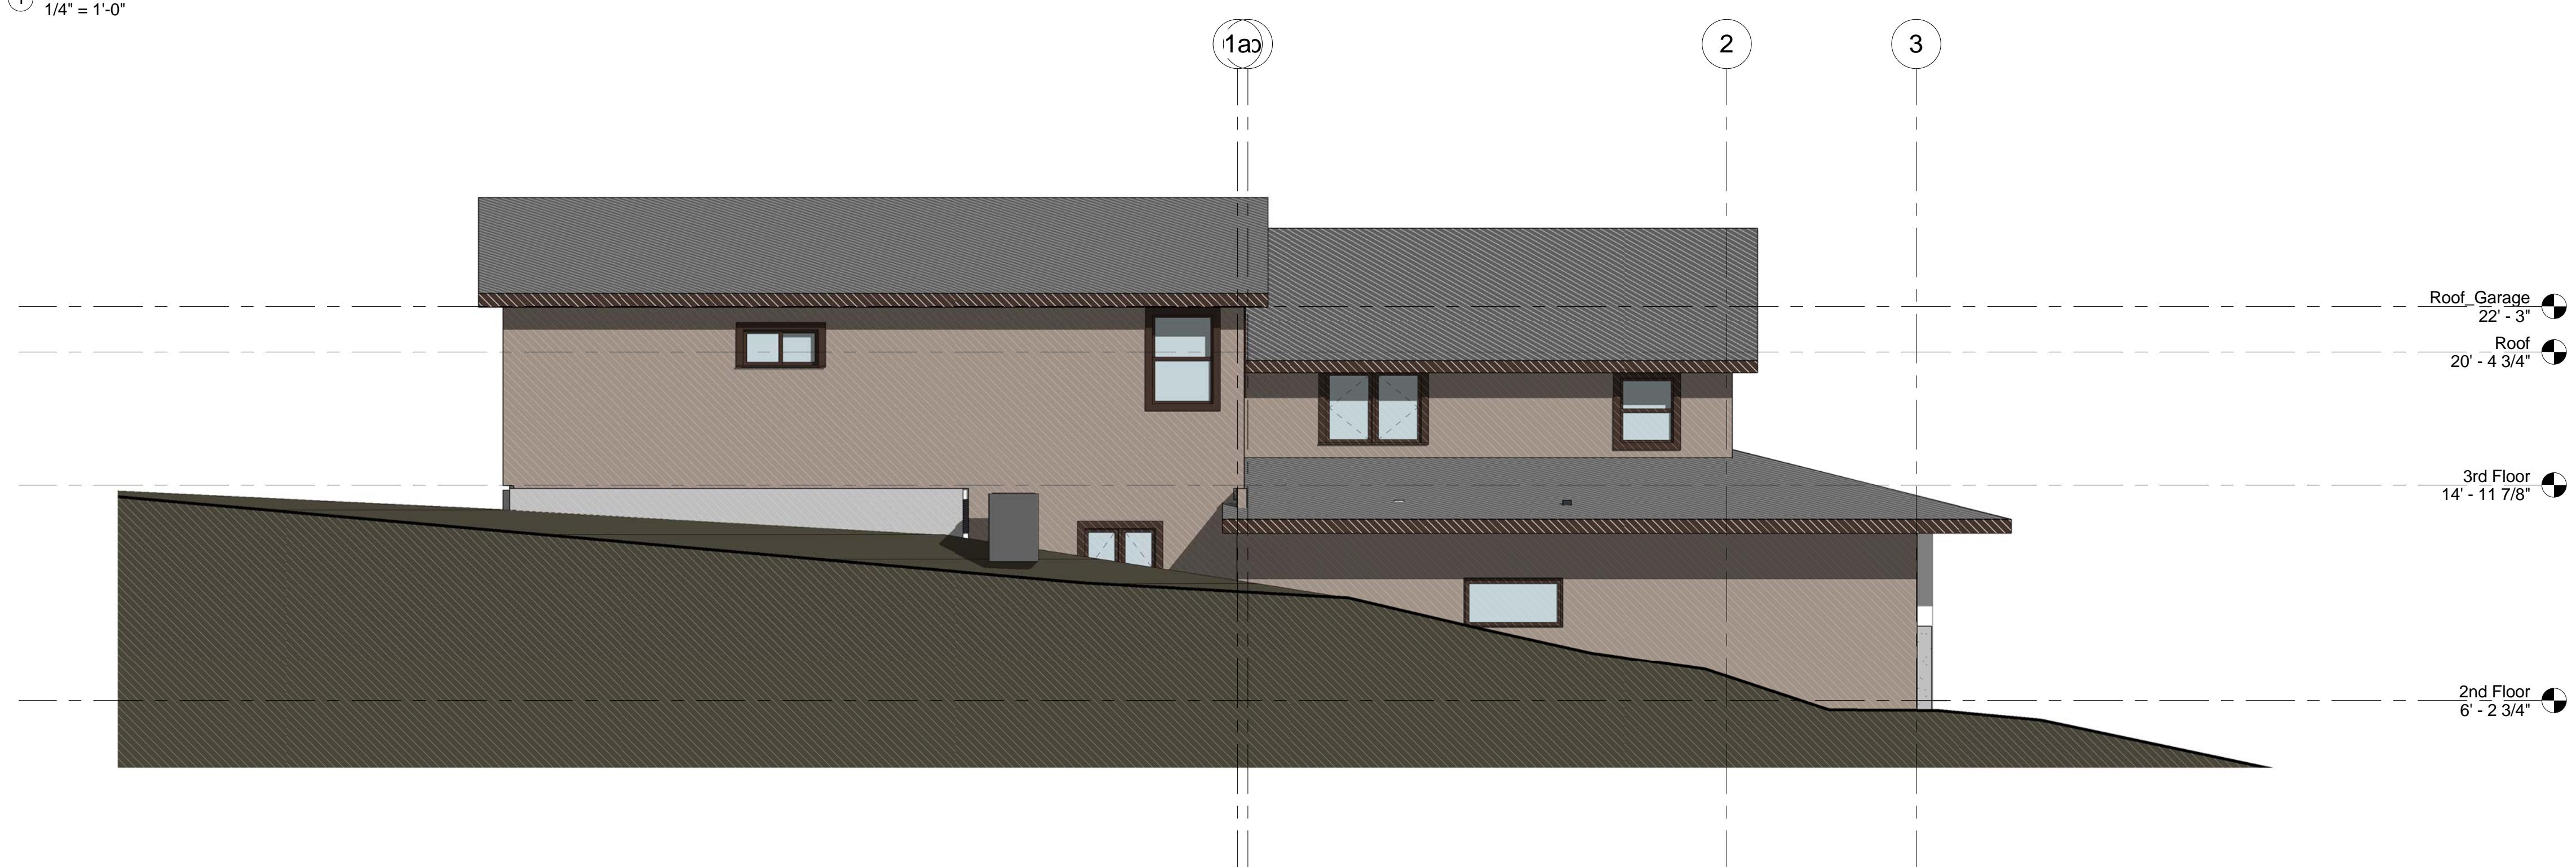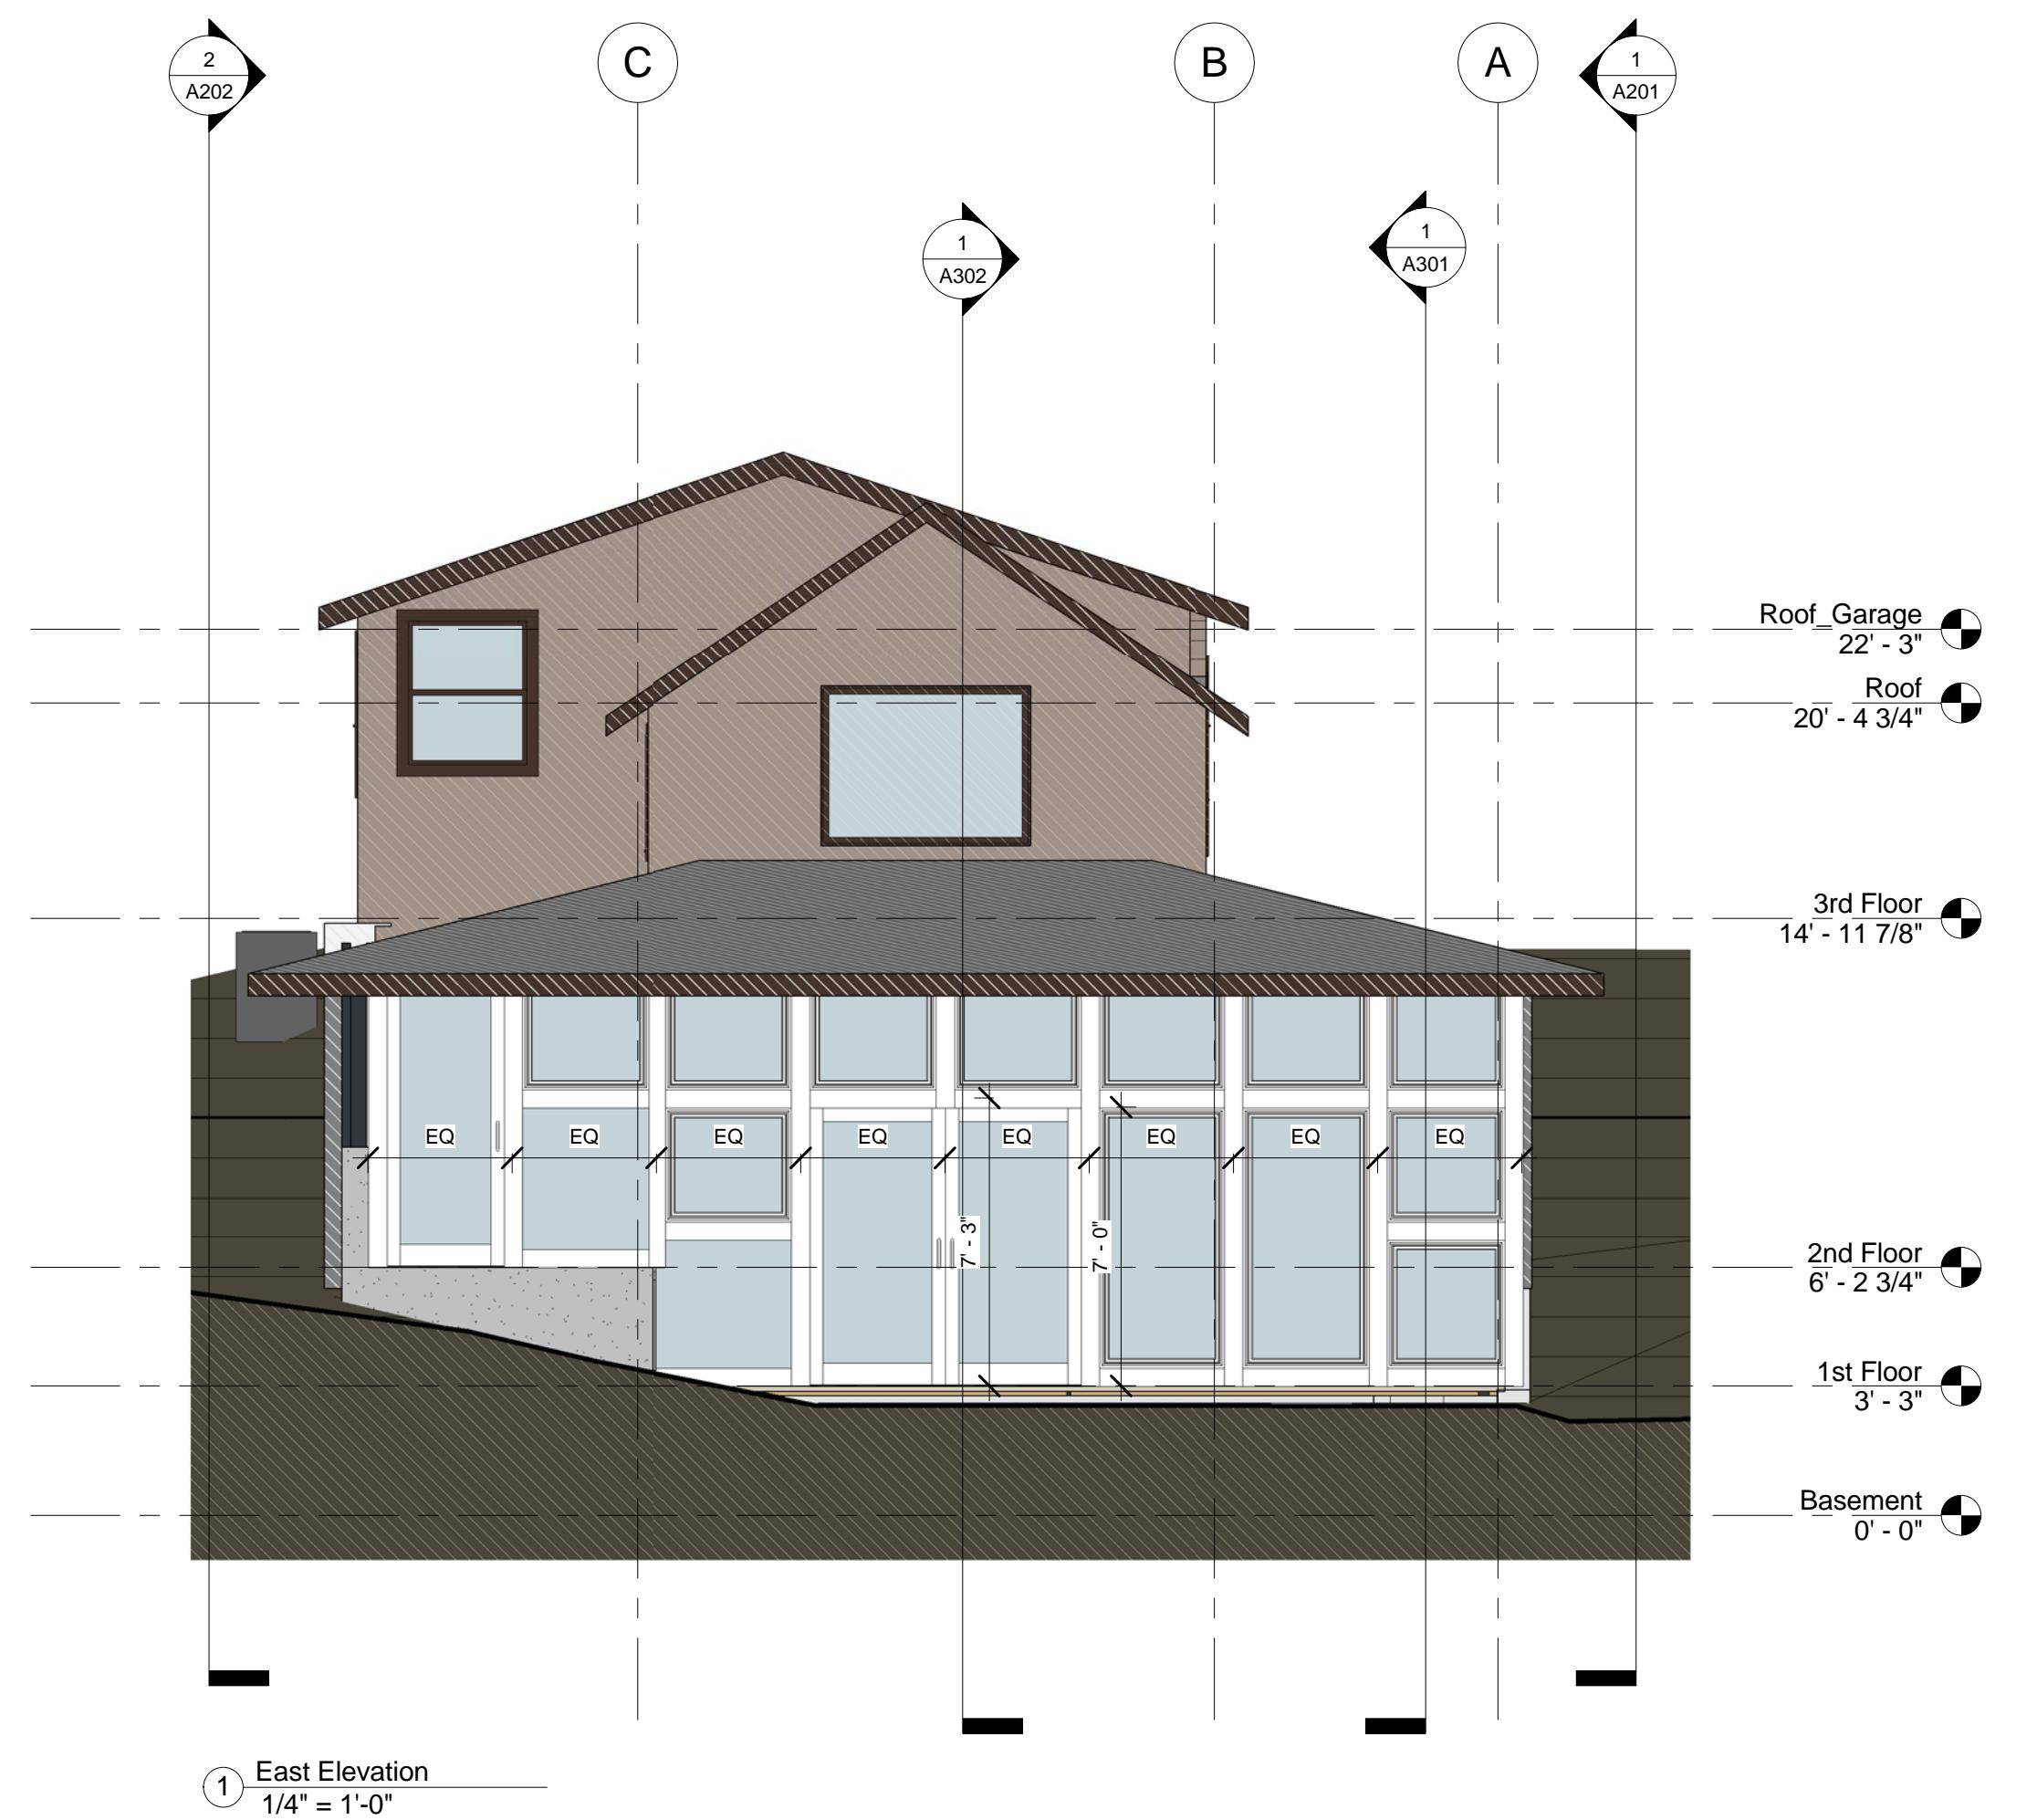



Elevations - South &  
East  
**A202**

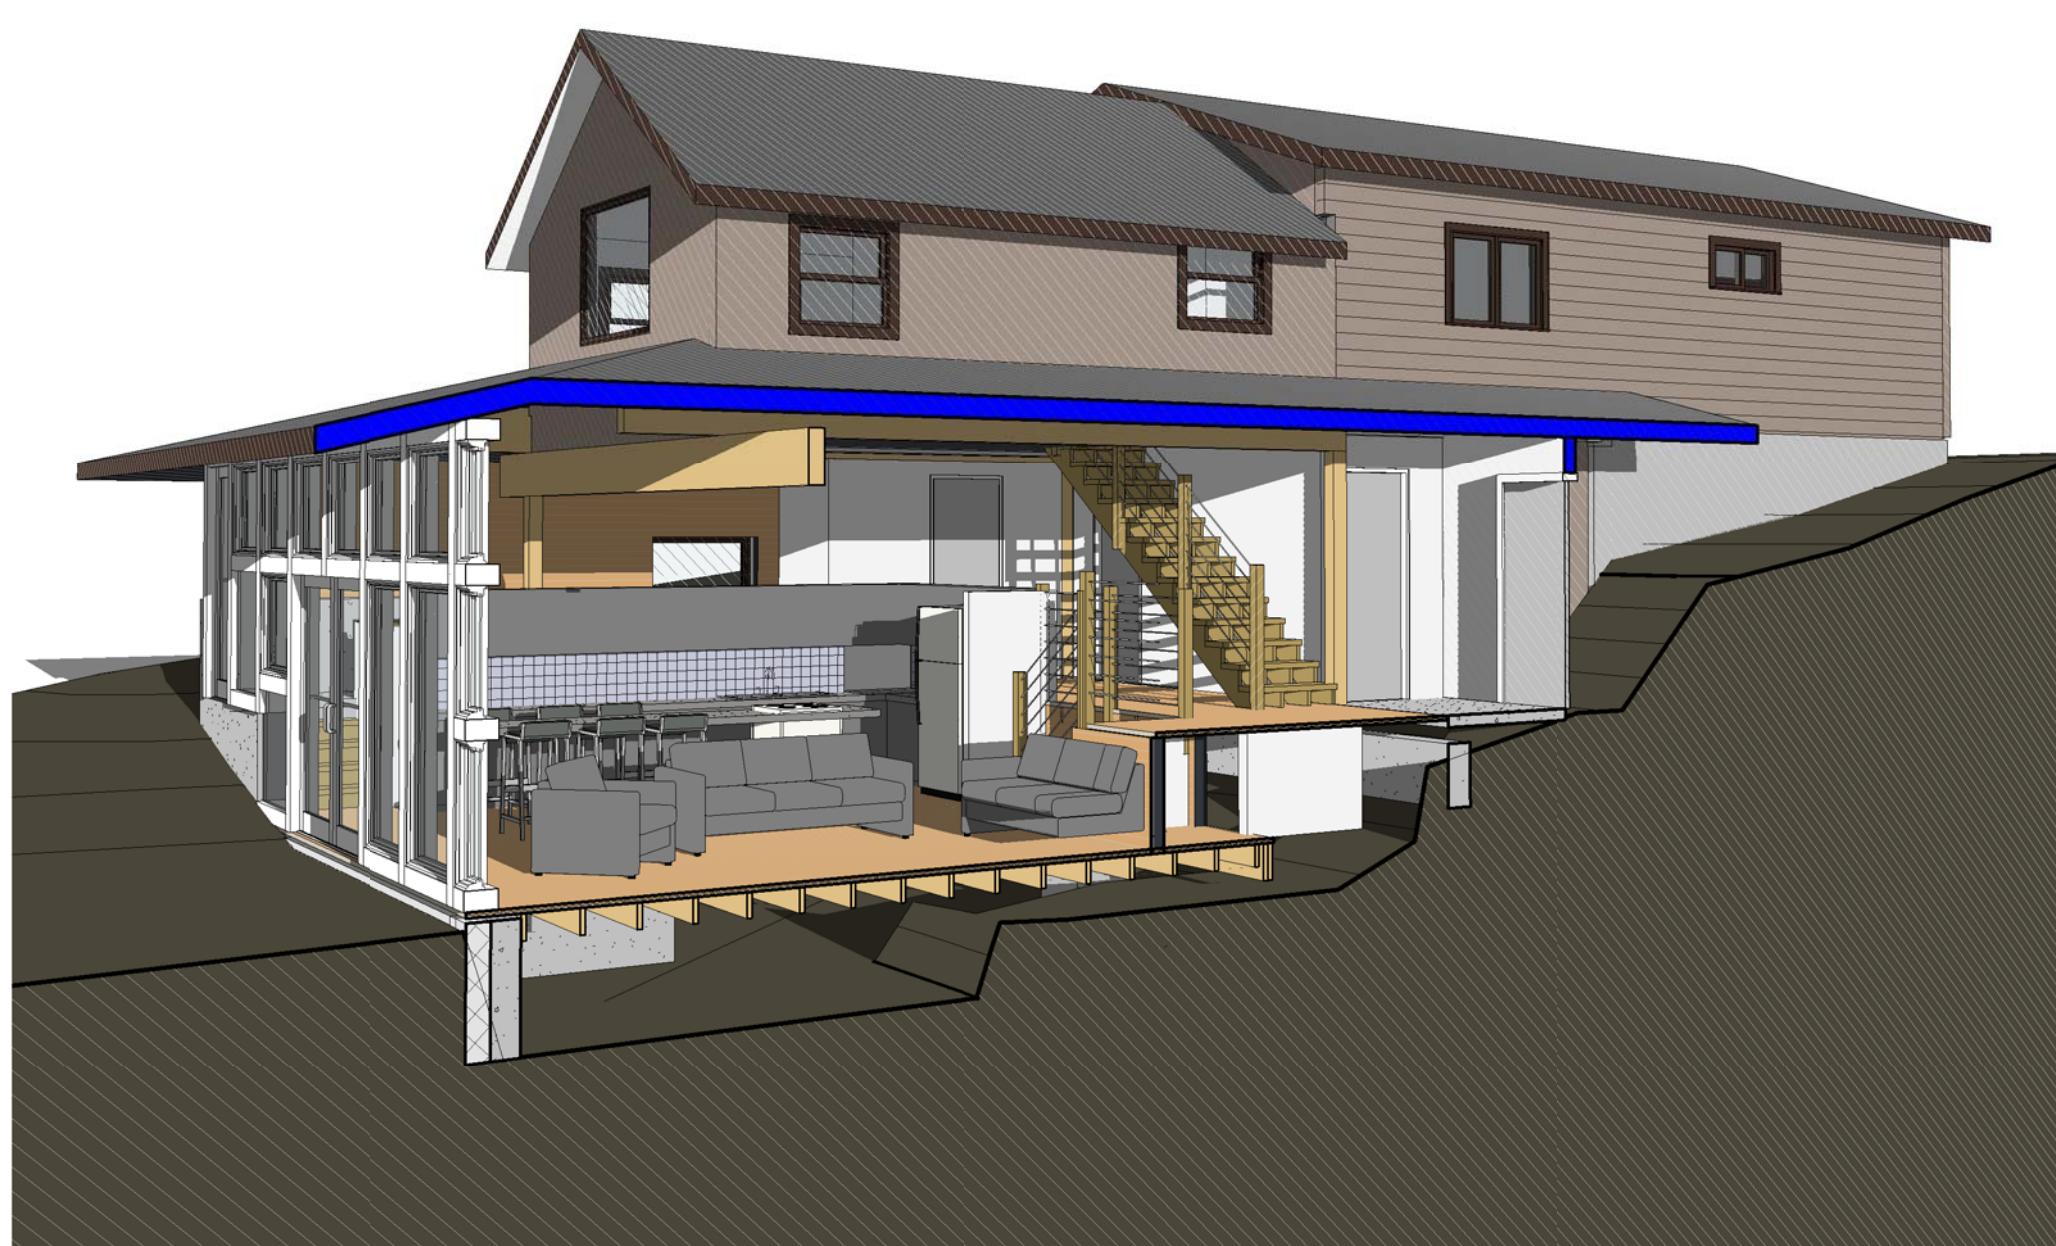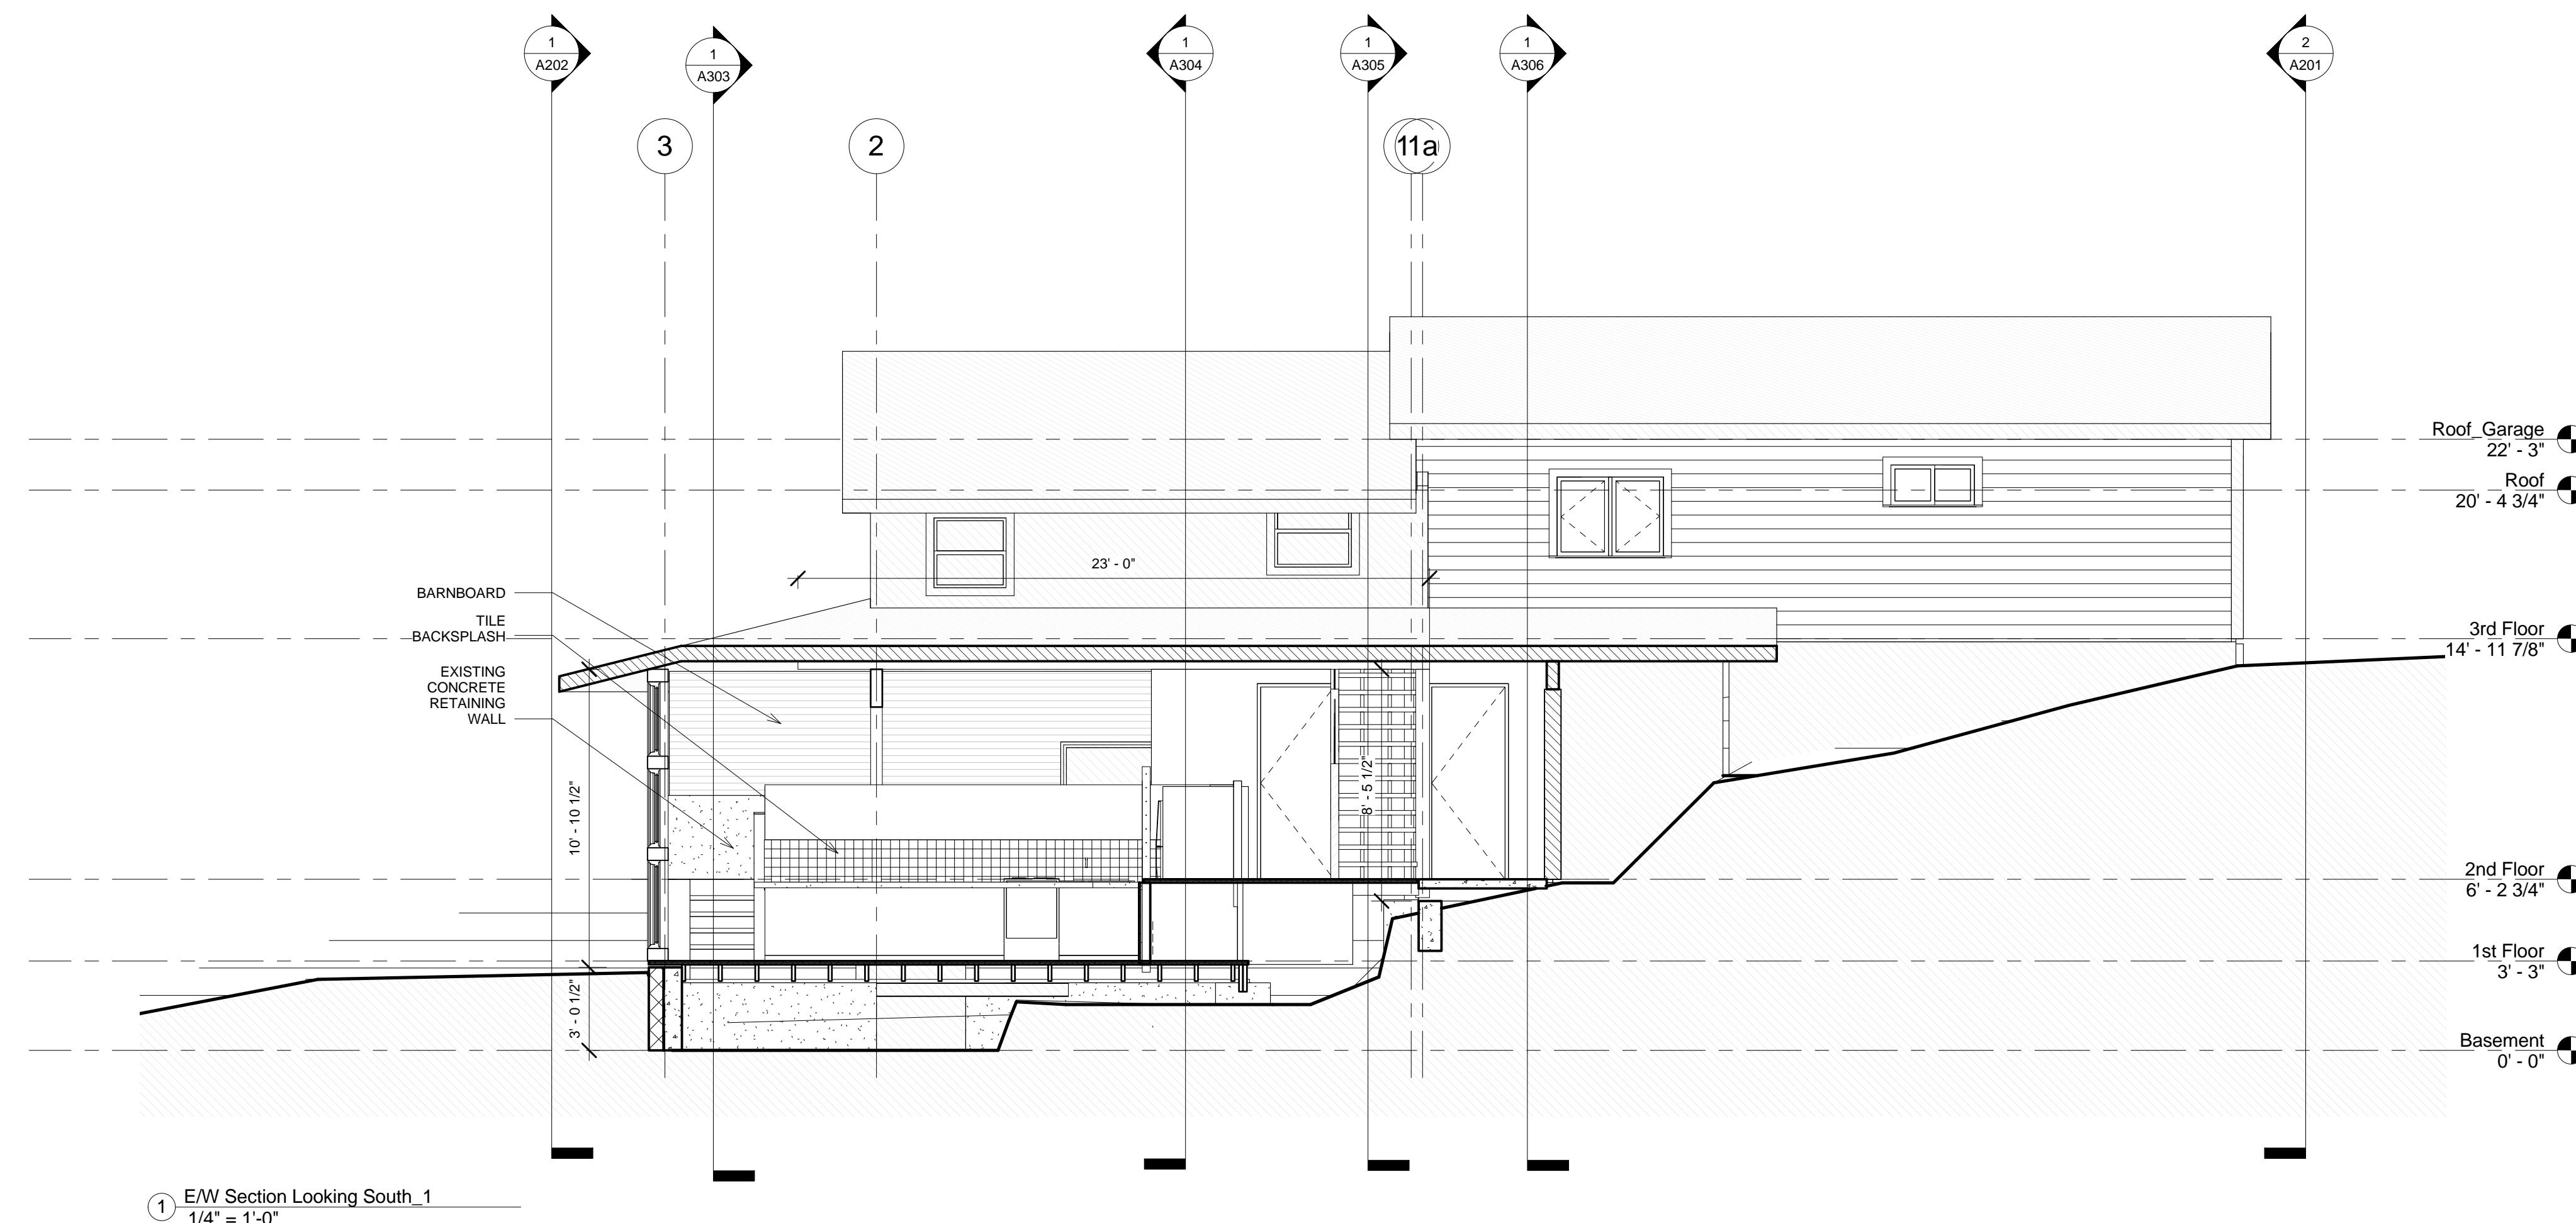

E/W Section  
Looking South  
**A301**

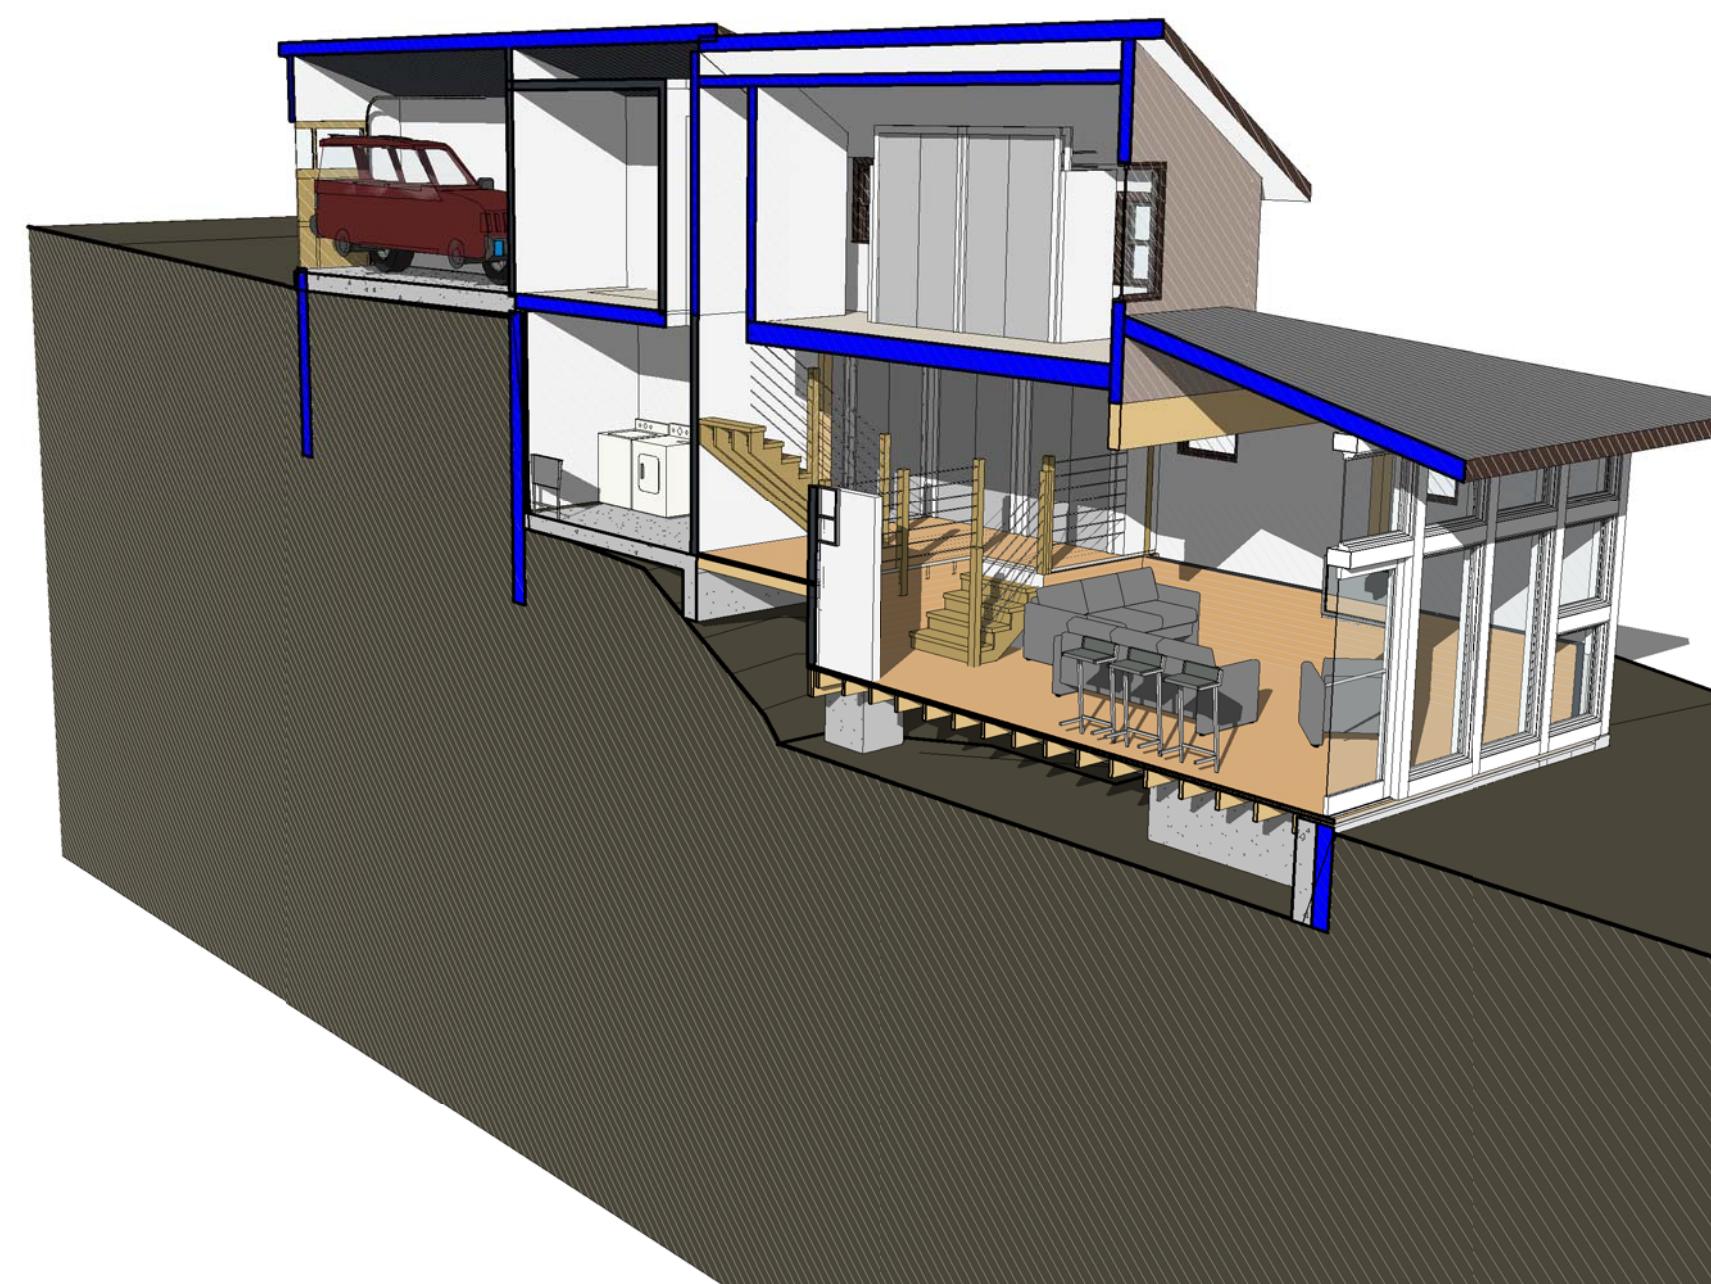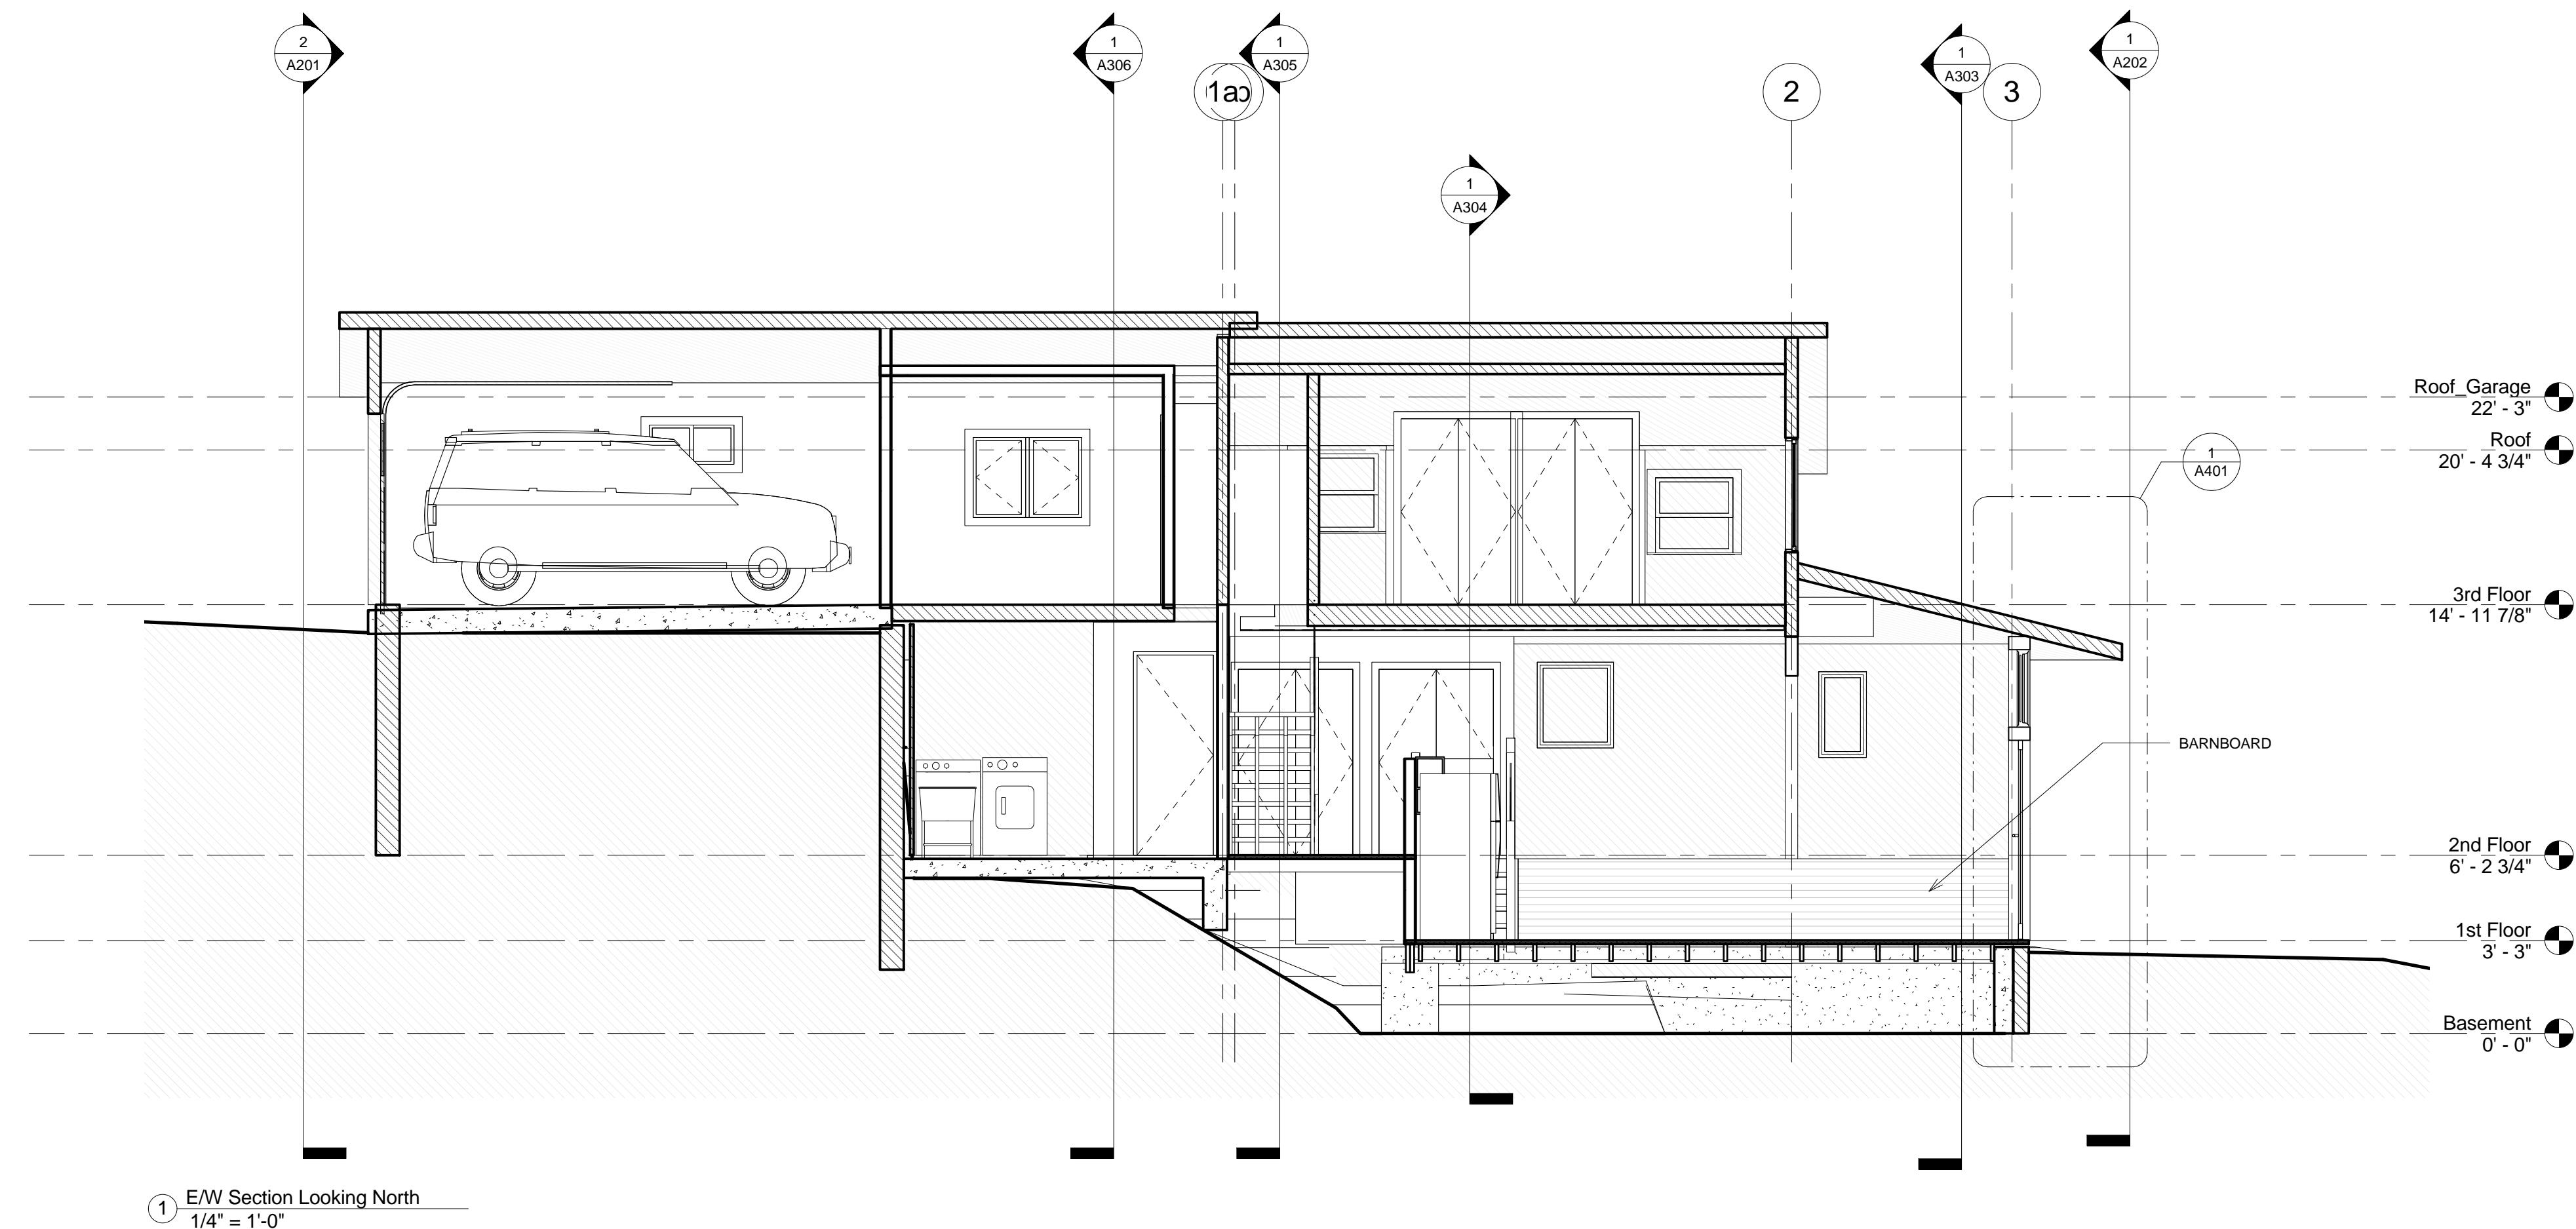

E/W Section  
Looking North  
**A302**

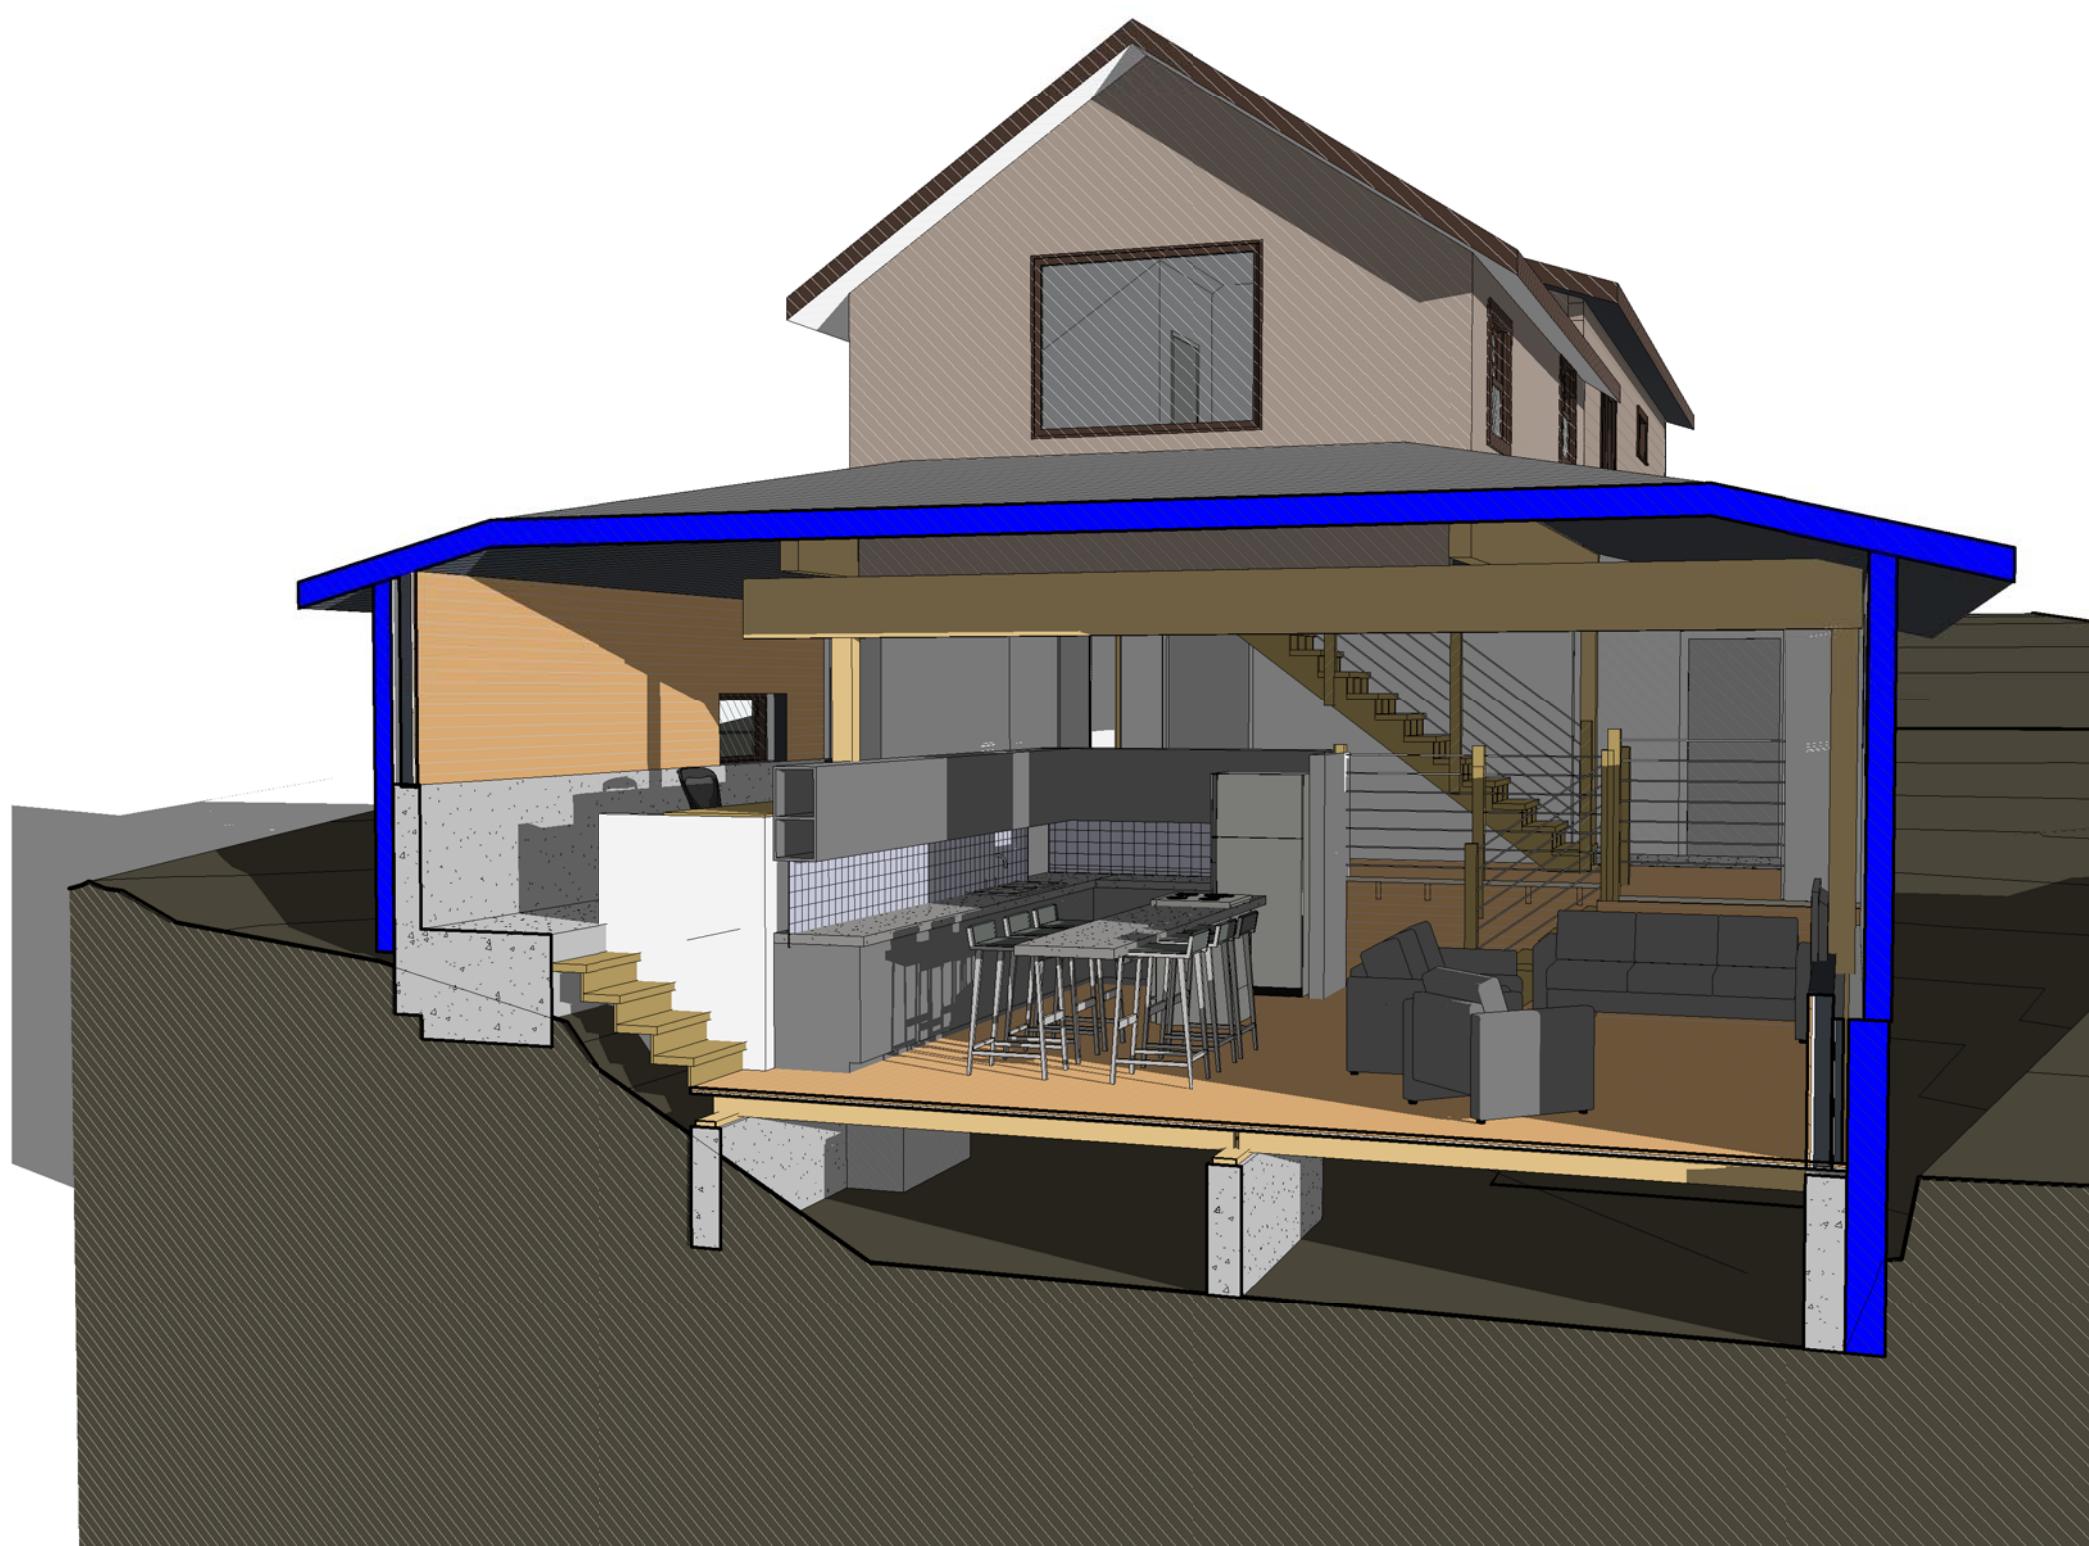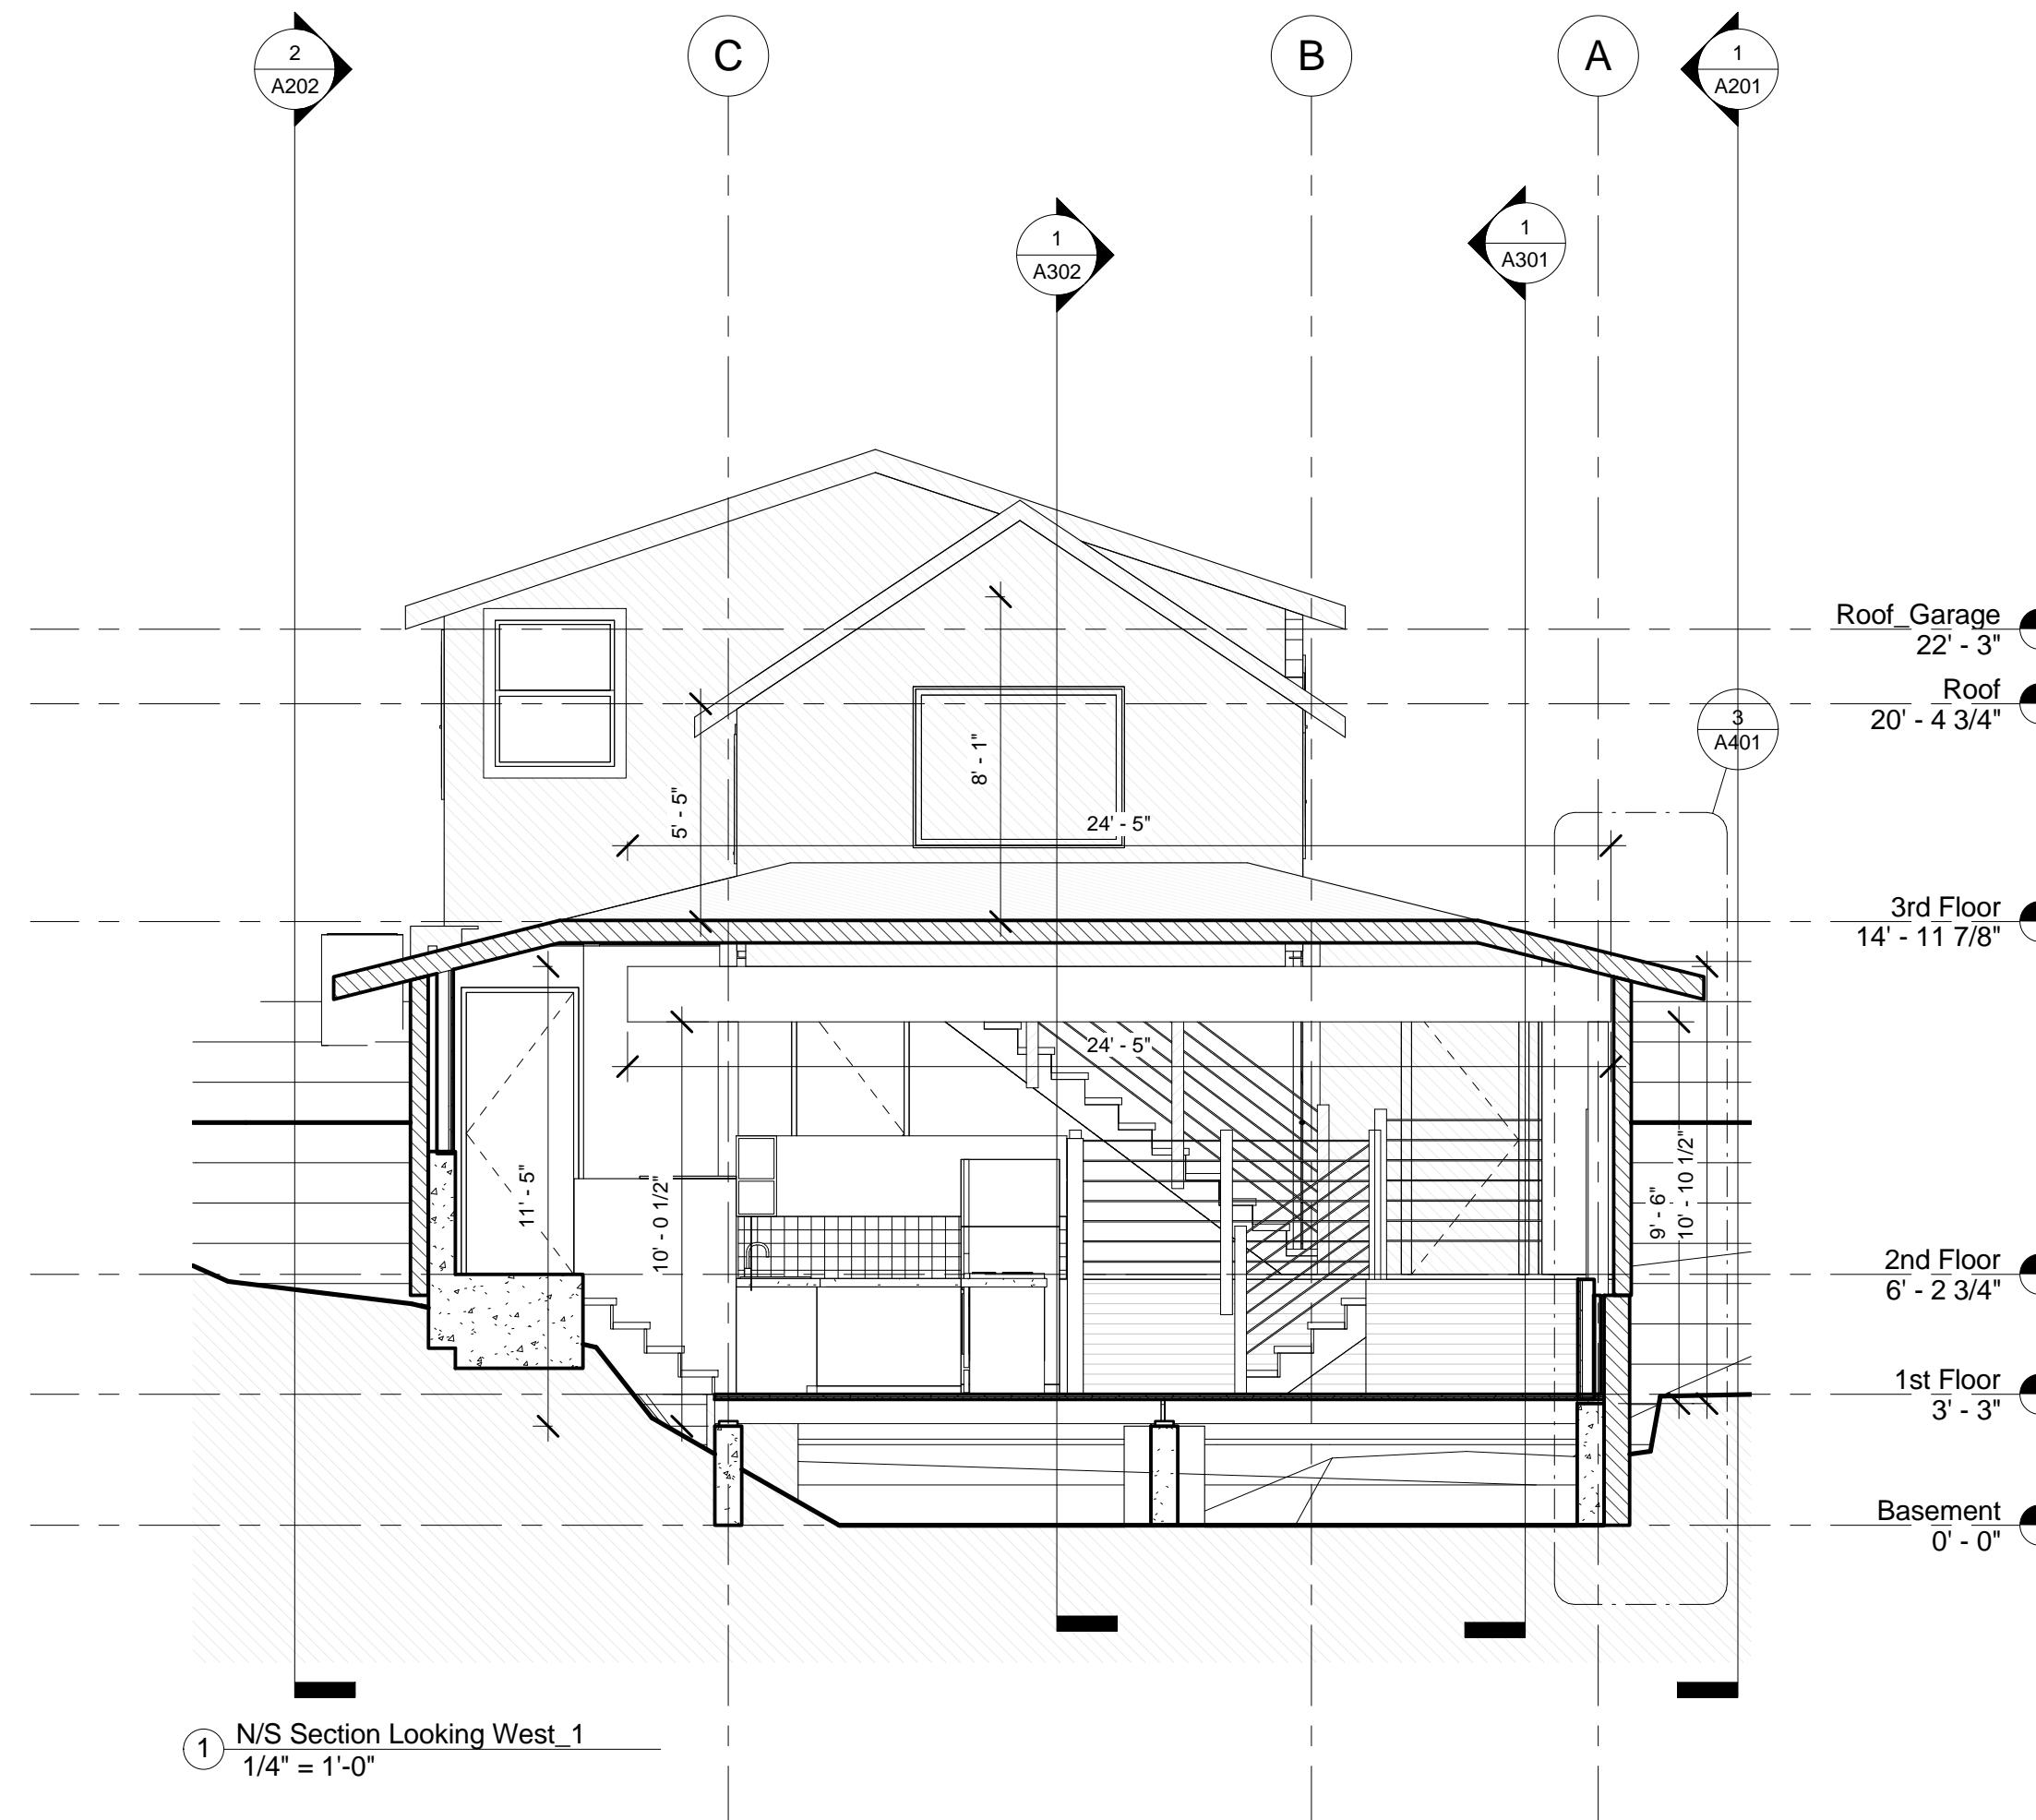


② N/S looking West\_1





③ Perspective - Looking West/South

N/S Section Looking  
West\_1  
**A303**

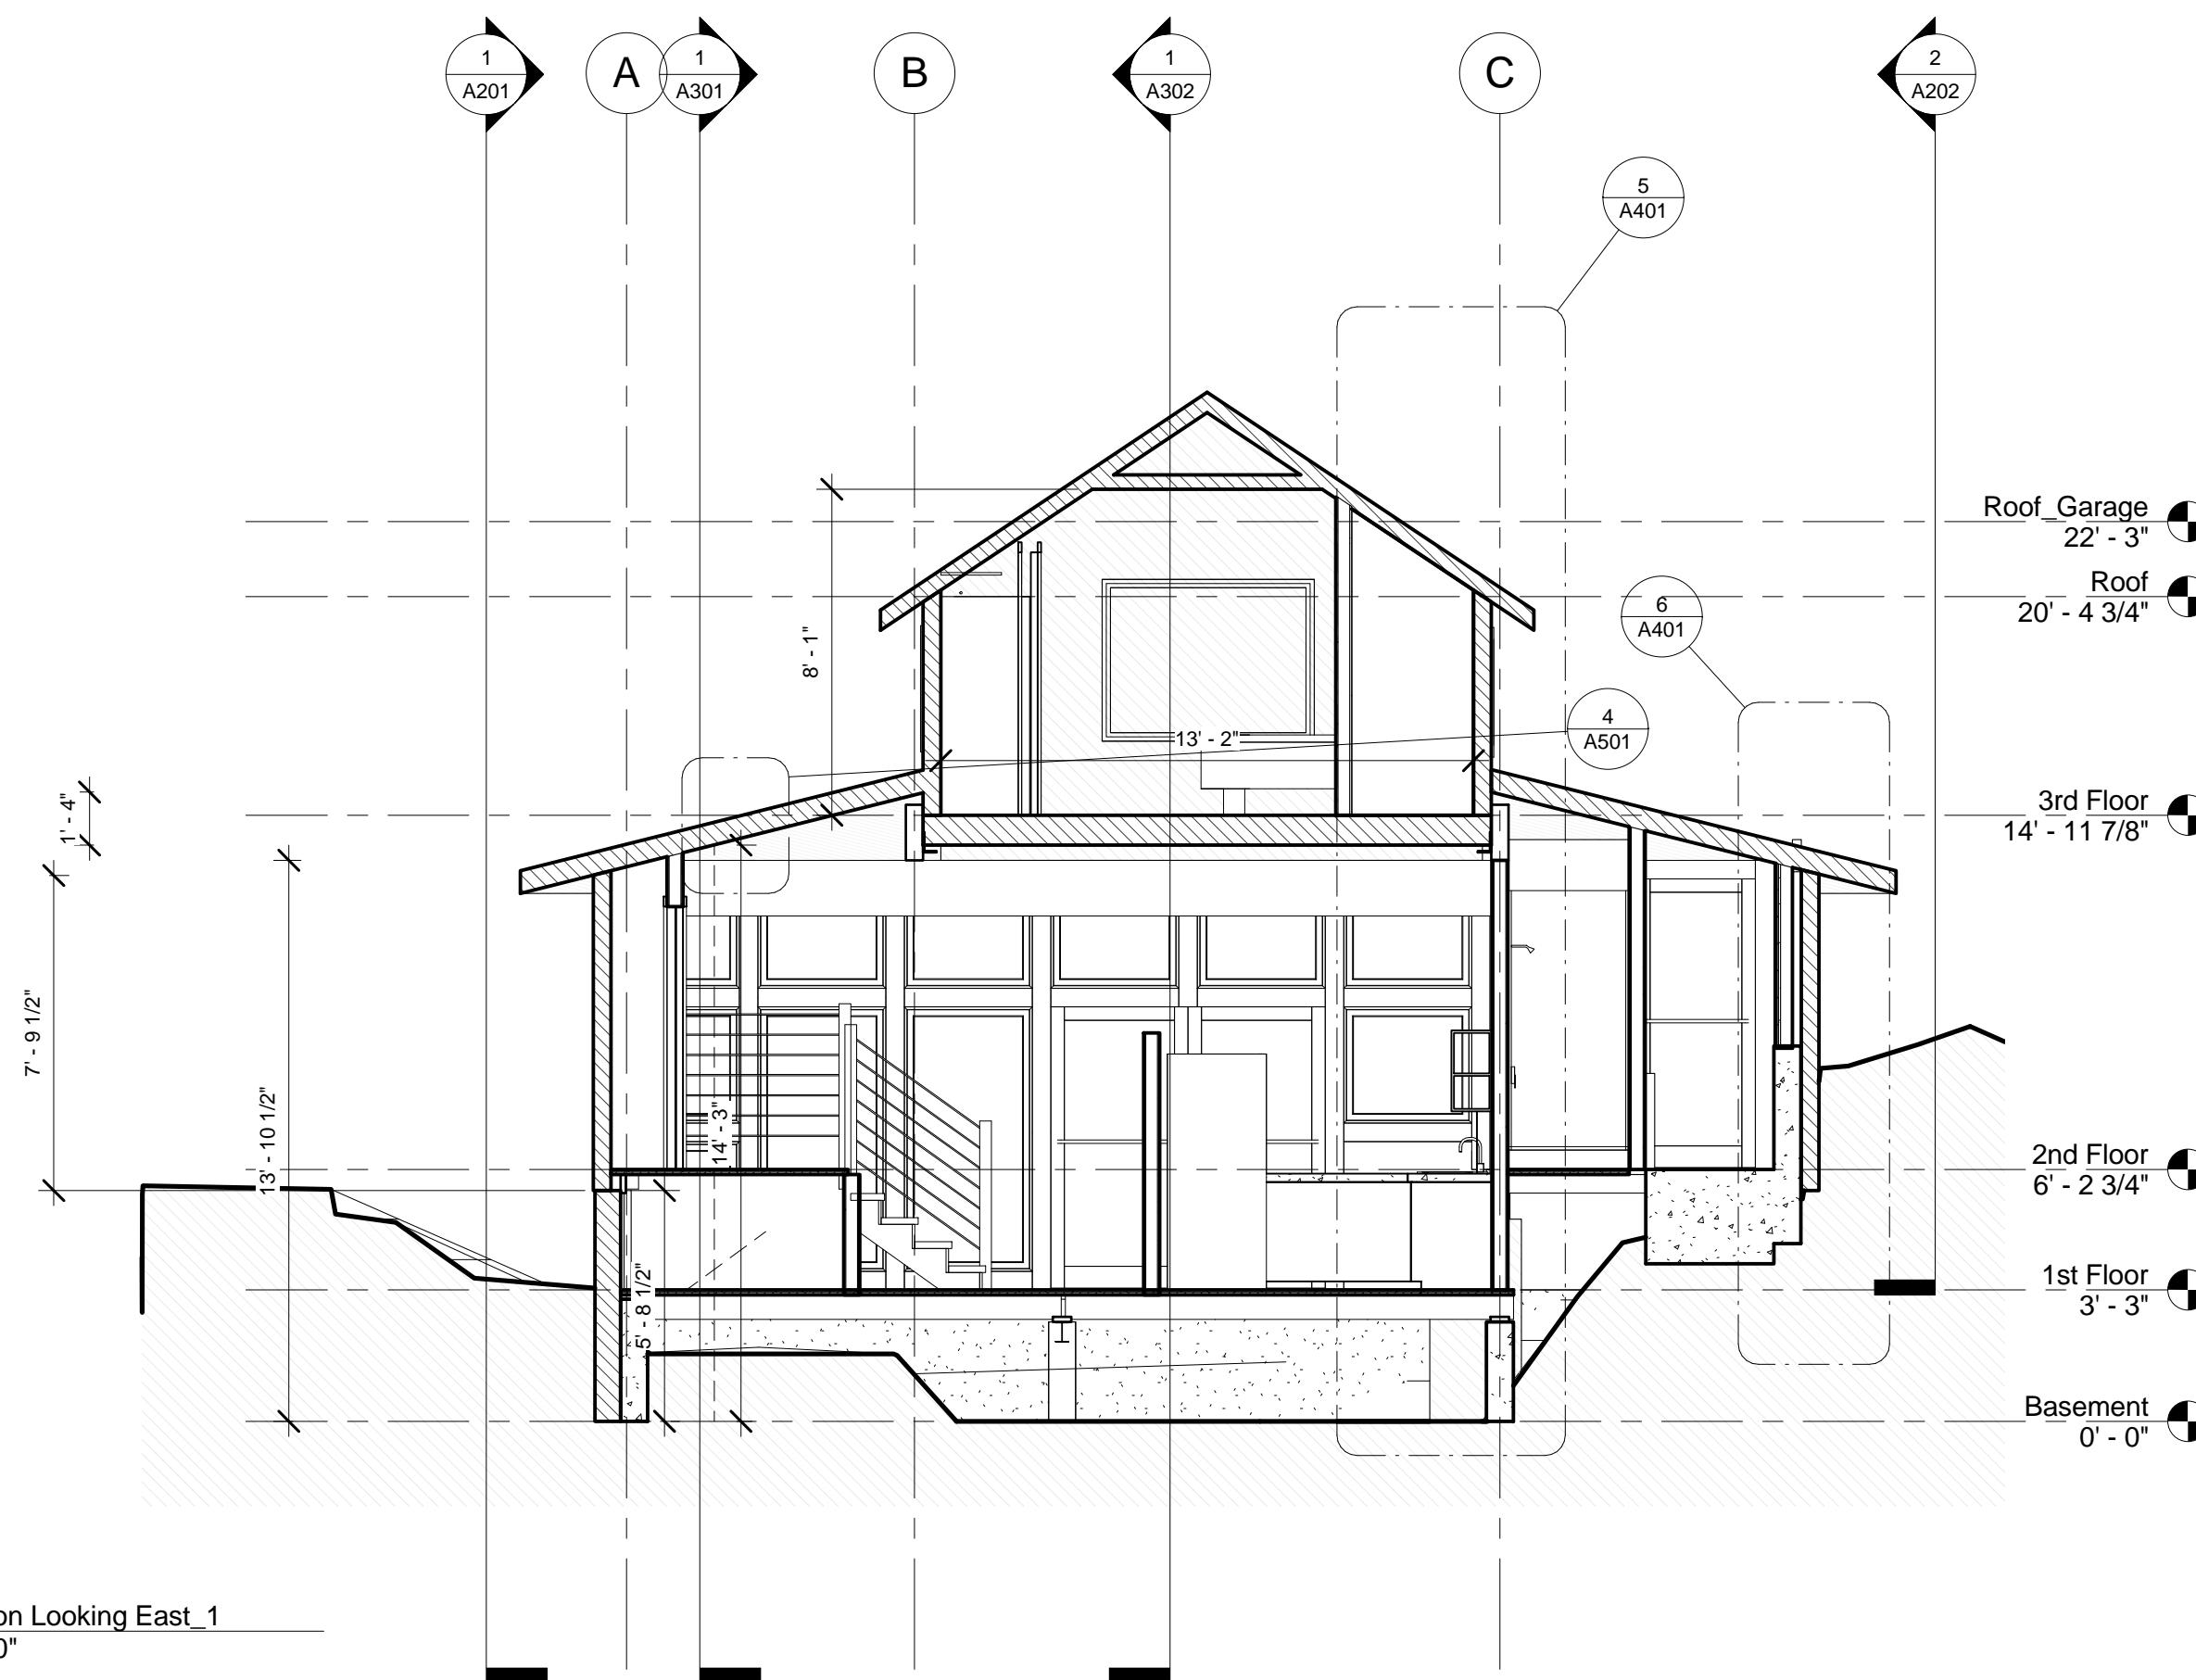

N/S Section Looking  
East\_1  
**A304**

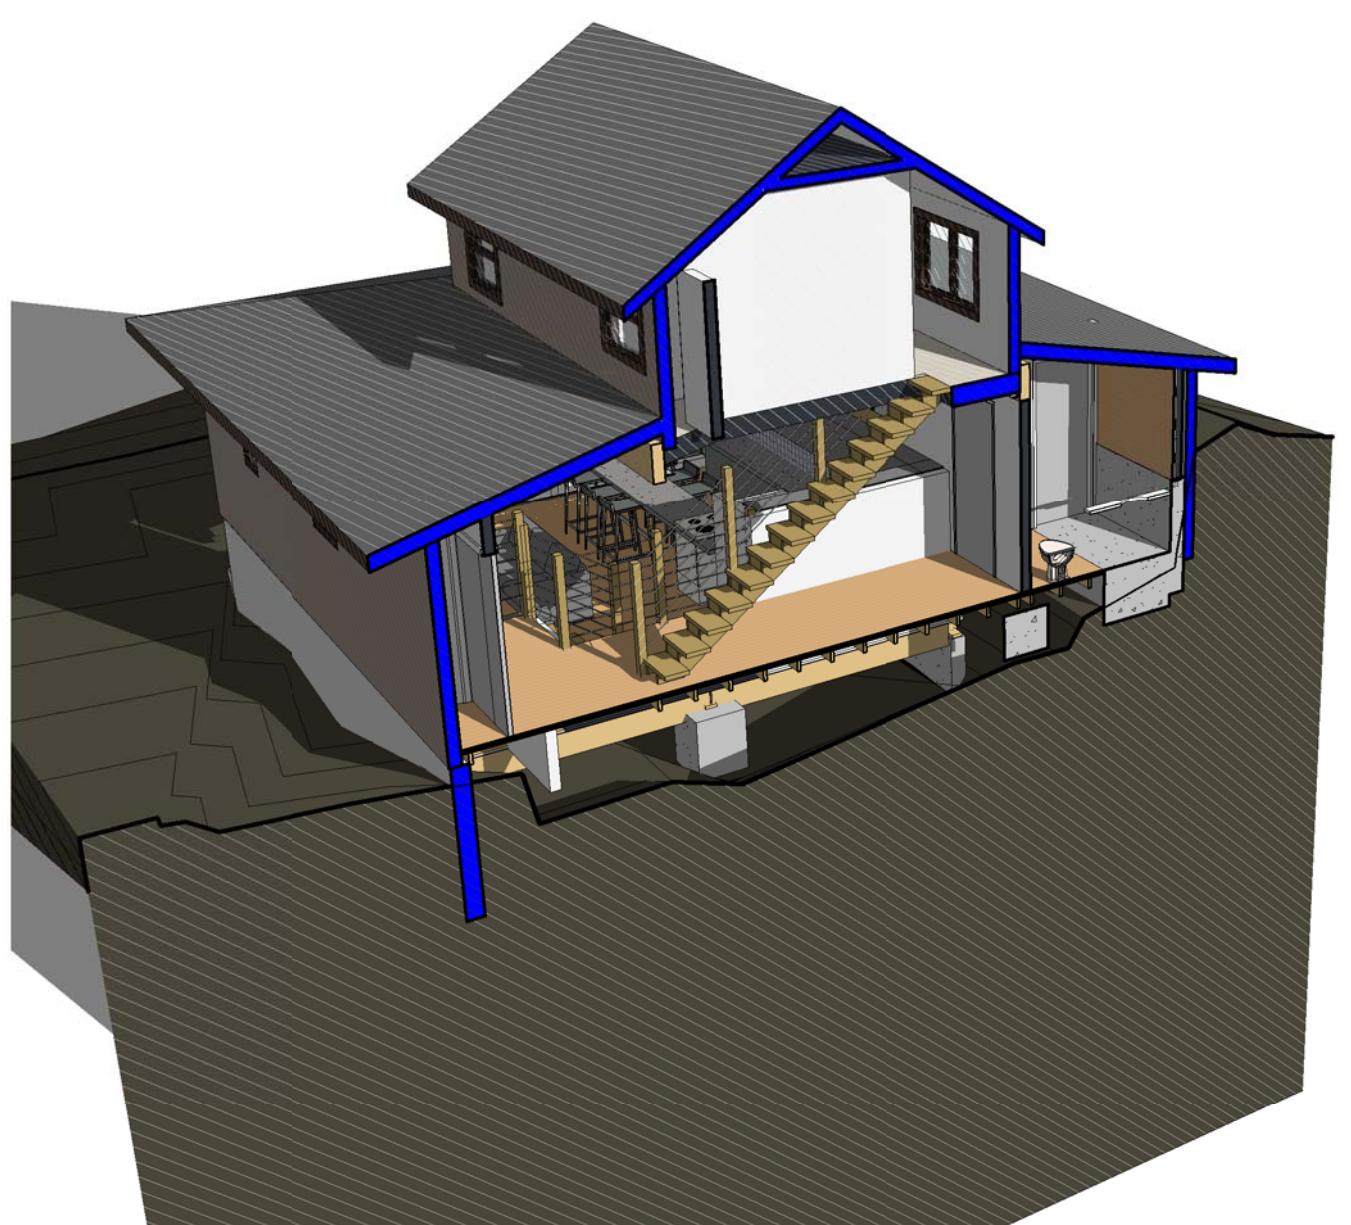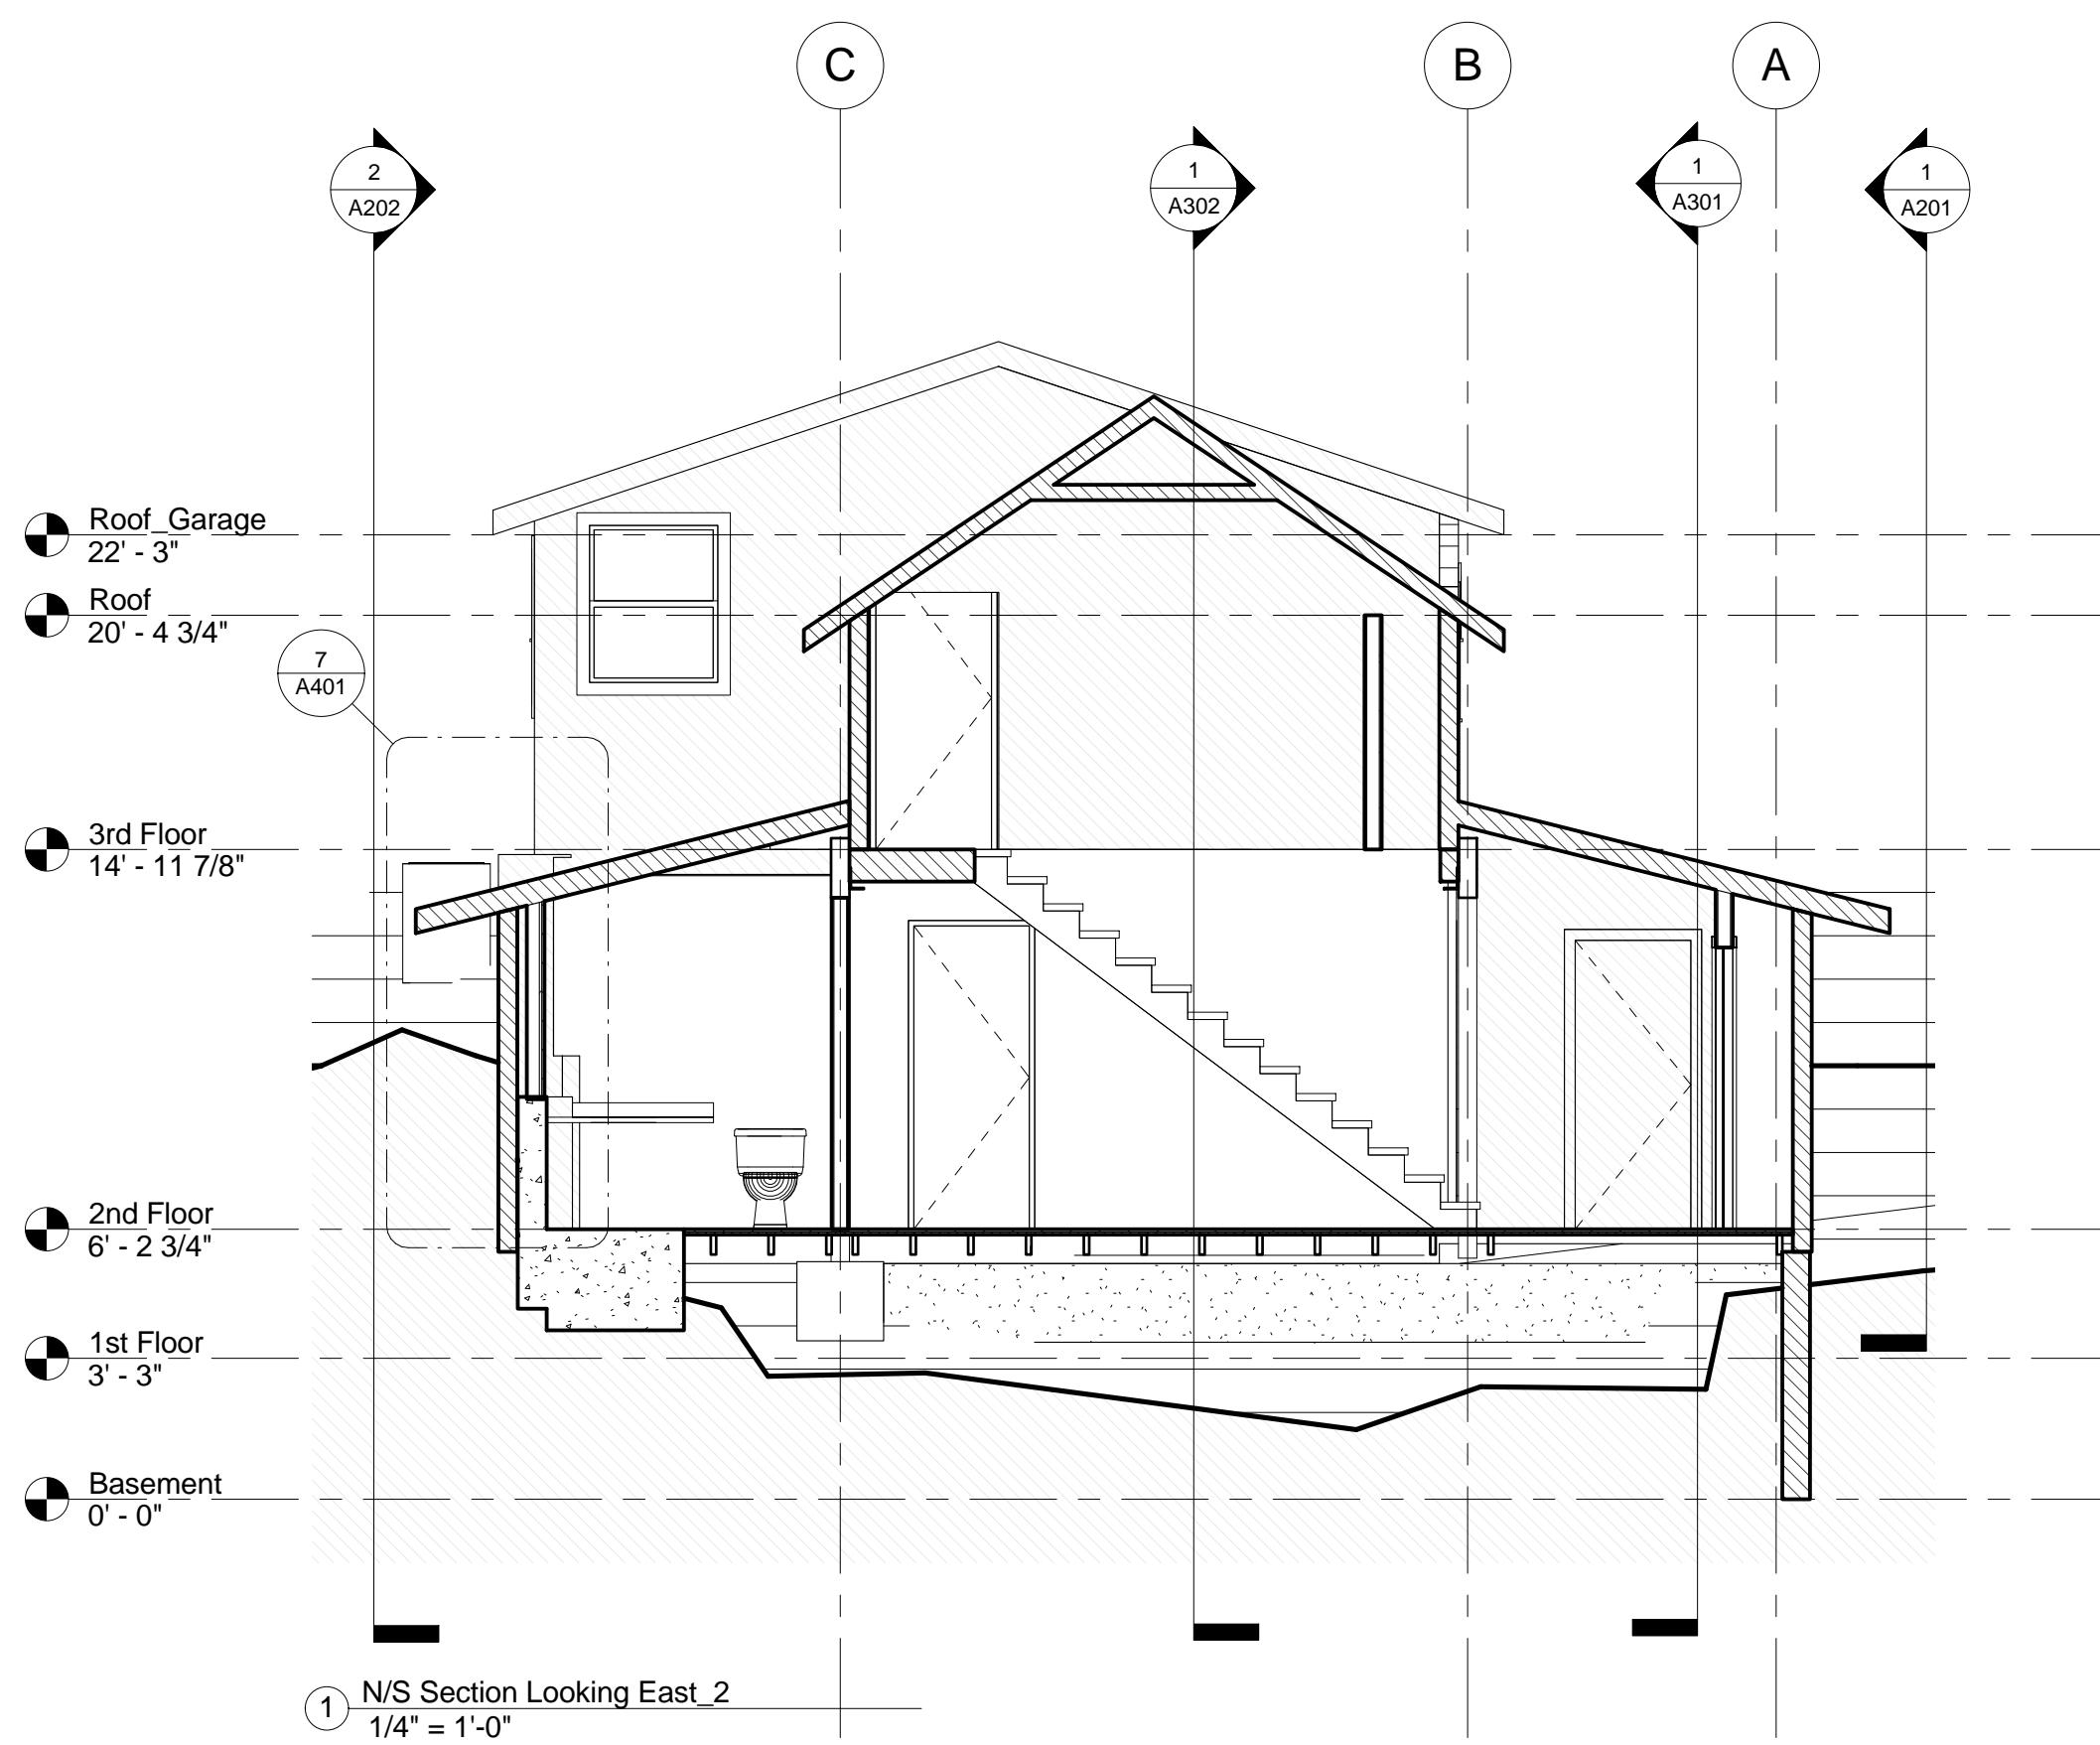

② Perspective - N/S Section Looking East\_2



③ Perspective - Looking South/East

N/S Section Looking  
East\_2  
**A305**